


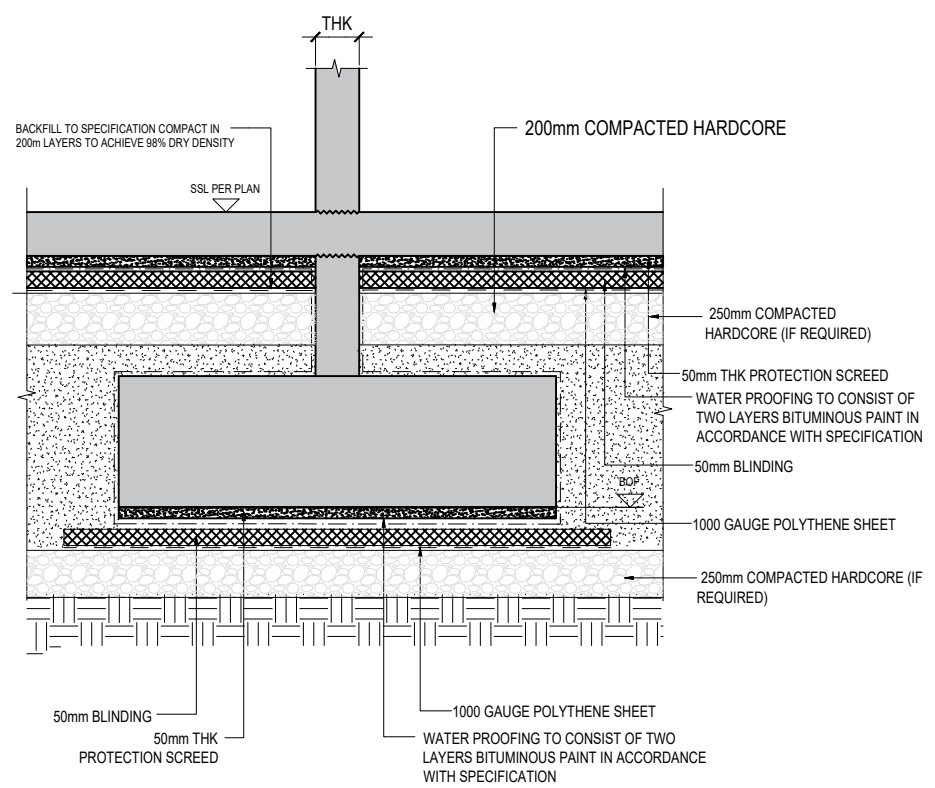


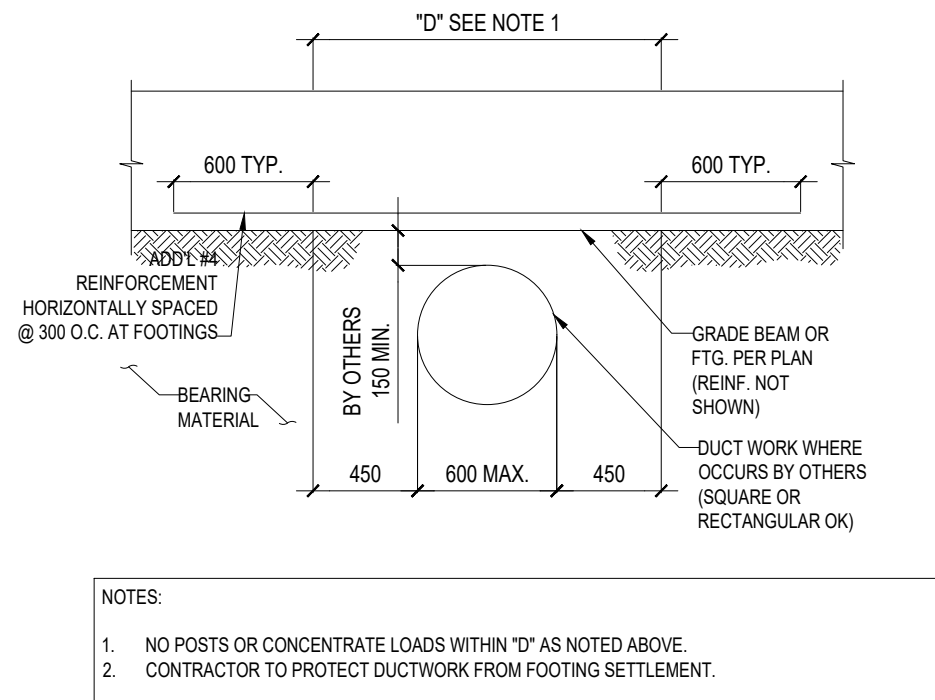

TYP. SLAB ON GRADE AND FOOTING
WATERPROOFING LAYERS
SCALE: N.T.S.

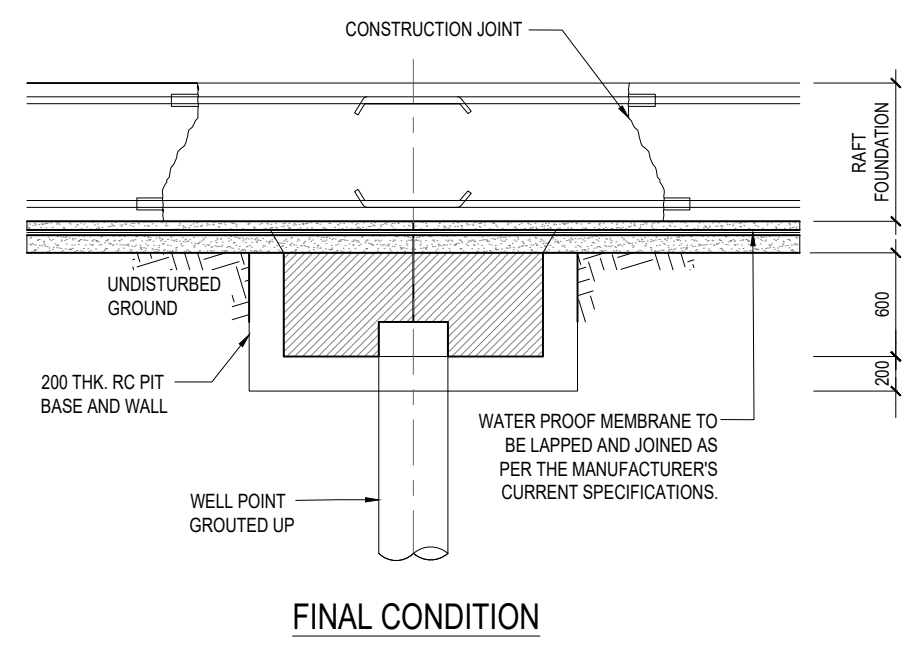


TYP. DUCT BELOW FOOTING OR GRADE BEAM
SCALE: N.T.S.

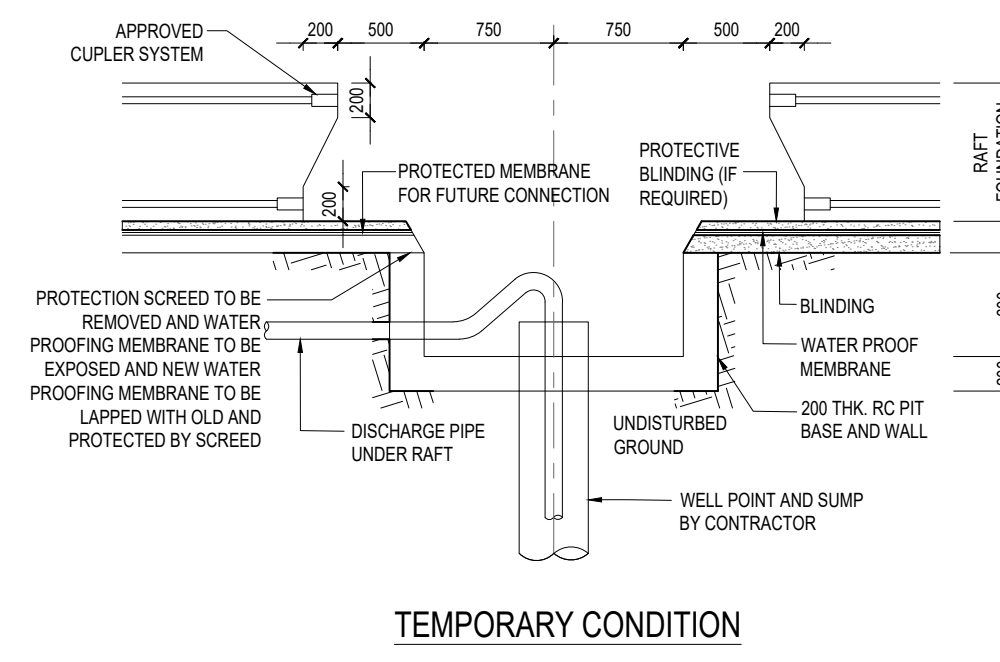


DE-WATERING SUMP IT IN RAFT FOUNDATION
SCALE: N.T.S.




INTERNAL CORNER DETAILS

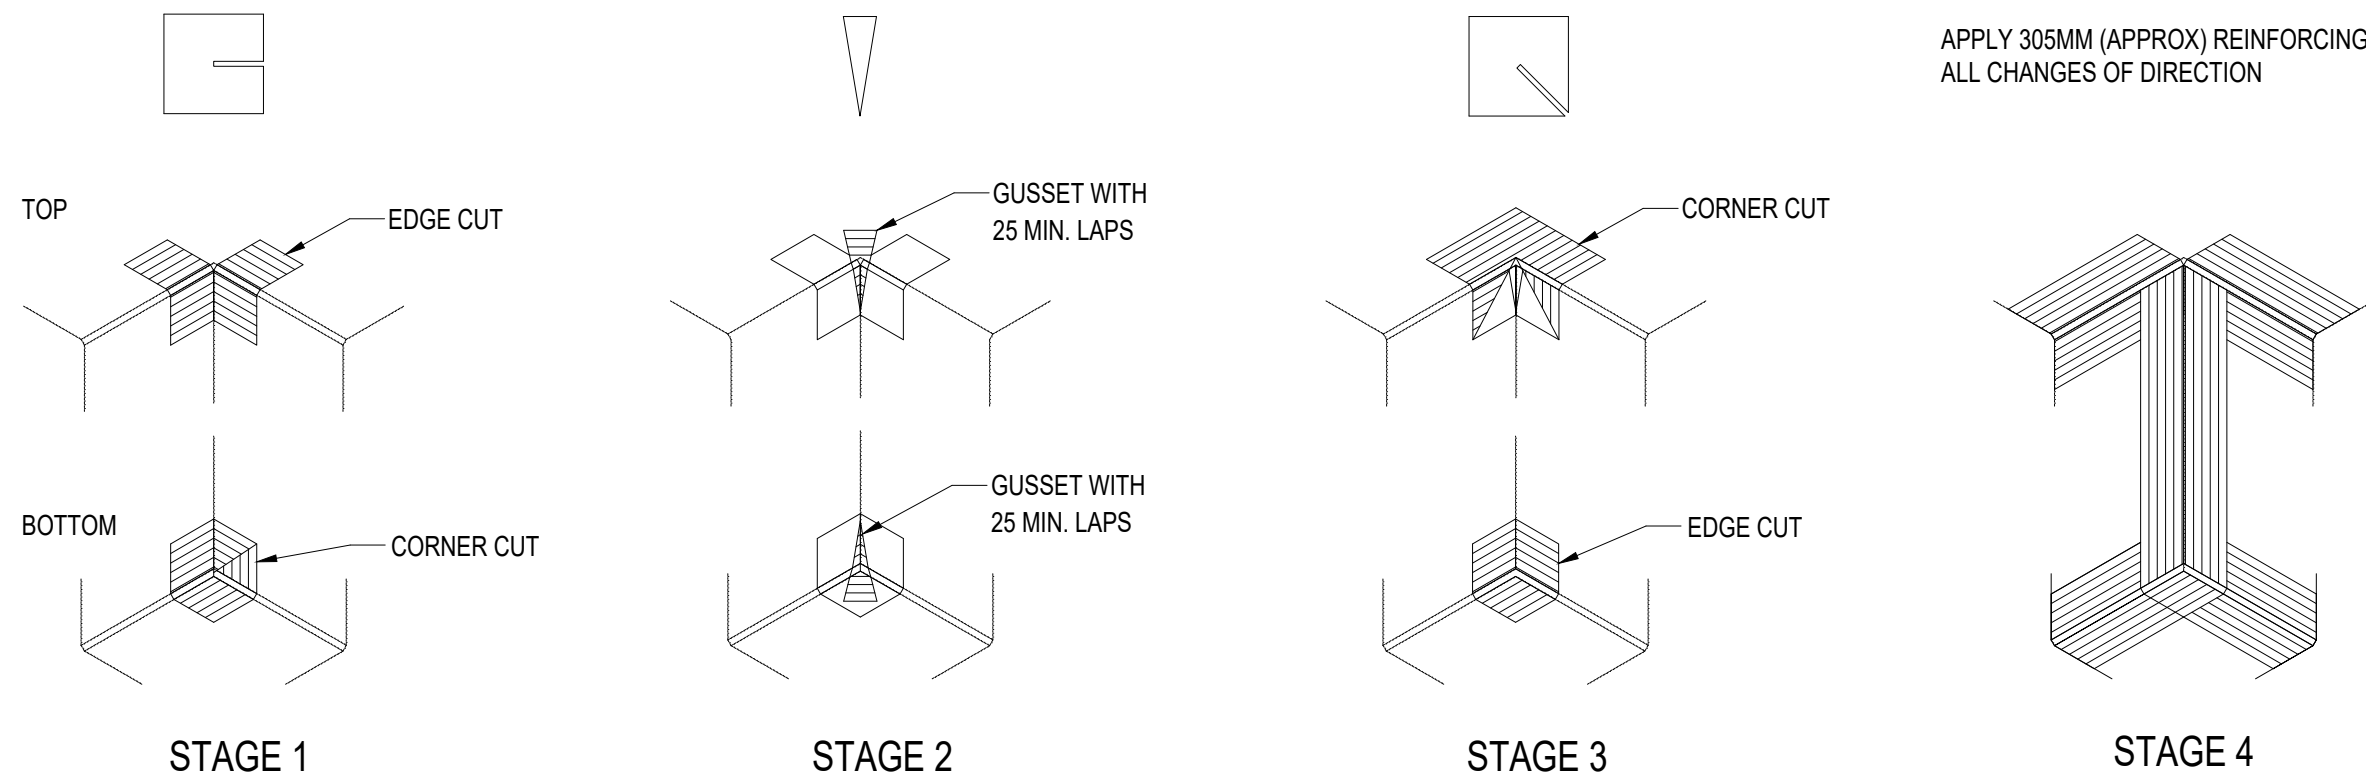

EXTERNAL CORNER DETAILS

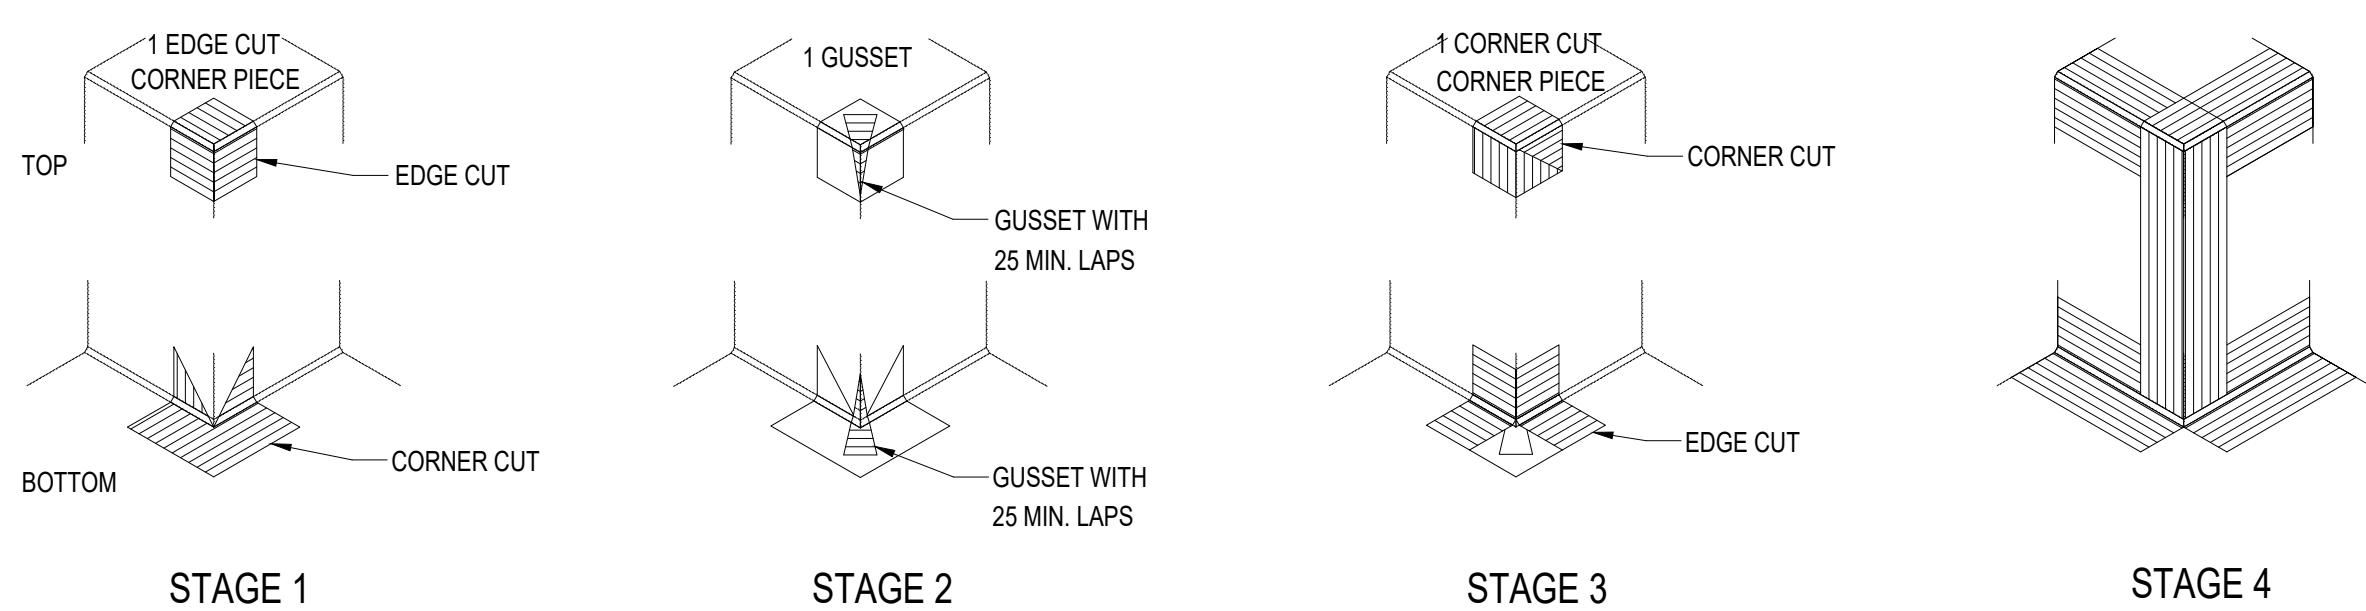


JOINT AT SLAB ON GRADE
SCALE: N.T.S.

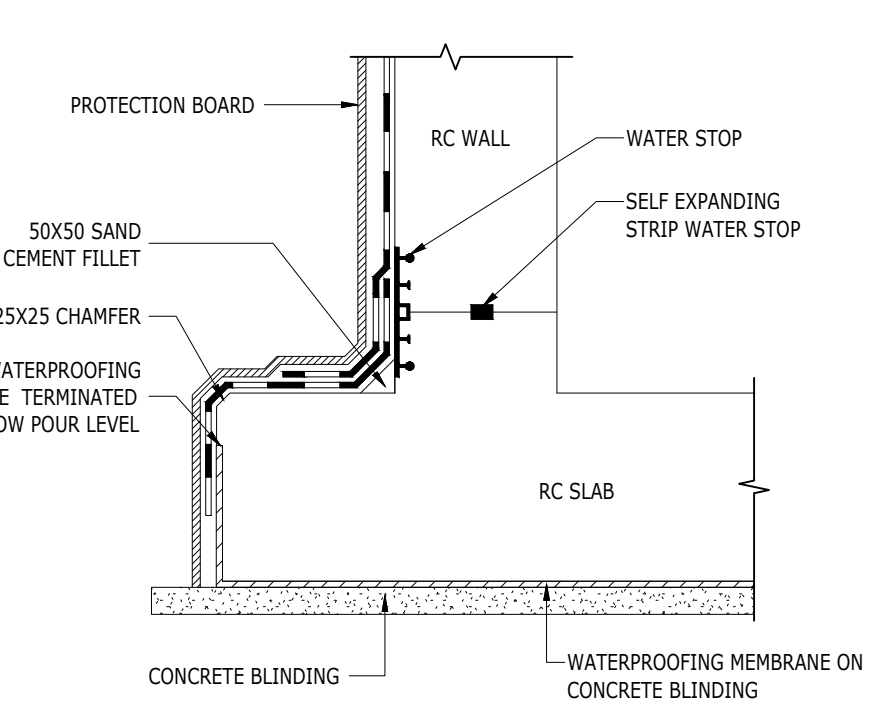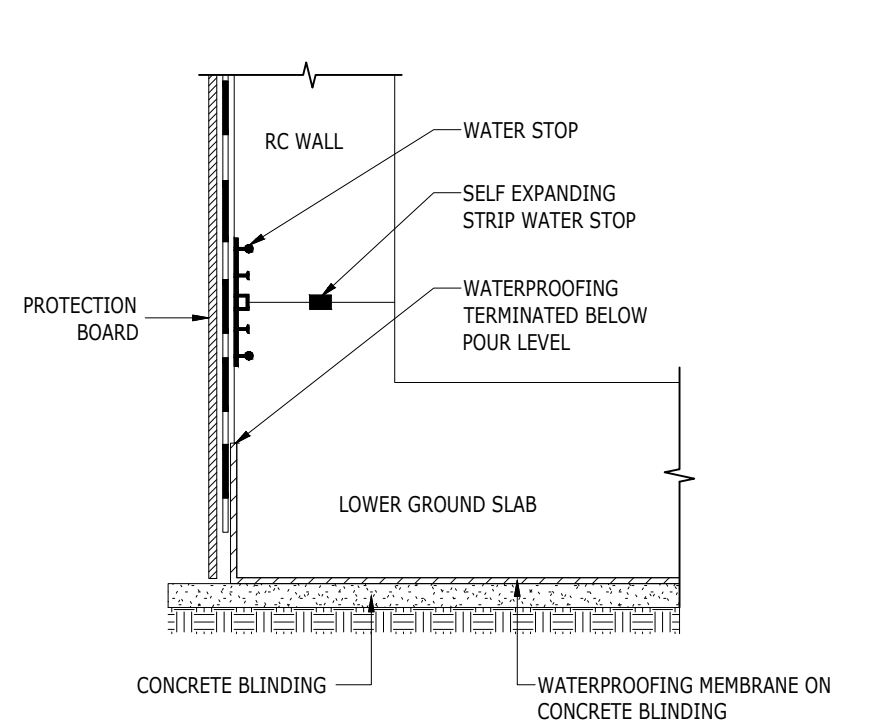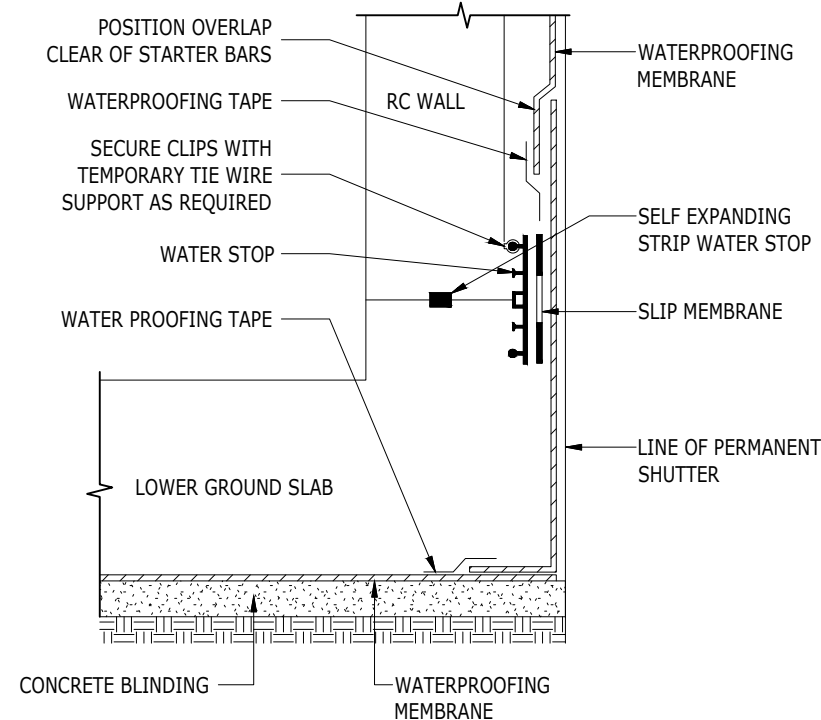

TYP. POUR STRIP IN RC SLAB / RAFT DETAIL
SCALE: N.T.S.

NON PT SLAB CONSTRUCTION JOINT
SCALE: N.T.S.

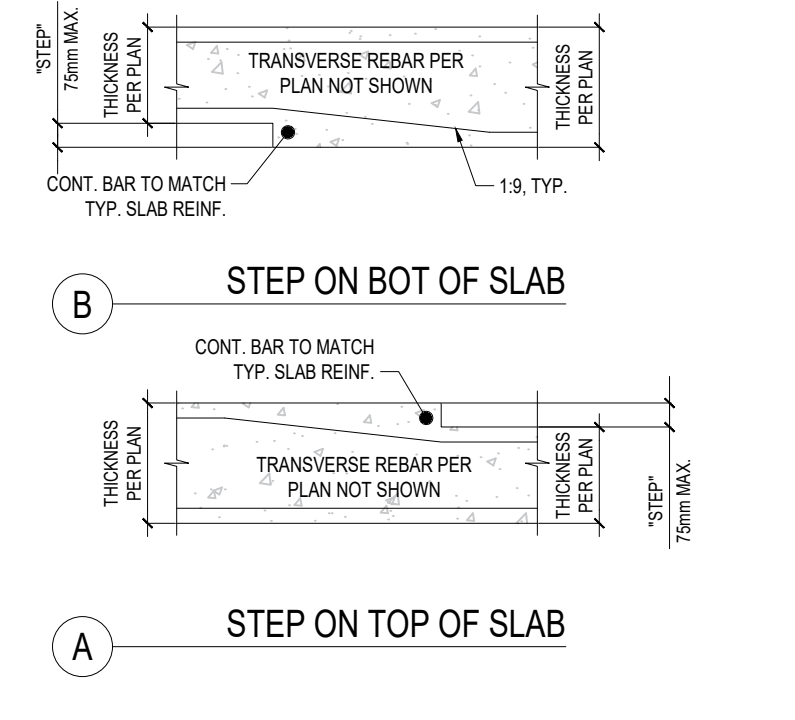


- NOTES:
- FOR LOCATION OF STEPS IN SLAB S.A.D.
 - THIS DETAIL APPLIES WHERE DIFFERENT SLAB THICKNESS IS SPECIFIED ON EITHER SIDE OF THE STEP, WHERE DIFFERENT THICKNESS IS NOT SPECIFIED, PROVIDE DETAILS PER "STEP IN CONCRETE SLAB"
 - WHERE "STEP" DIMENSION IS GREATER THAN 75mm, PROVIDE DETAILS PER "STEP IN CONCRETE SLAB" DETAIL

TYPICAL CONCRETE SUBSTRUCTURE WATERPROOFING DETAILS
SCALE: N.T.S.

CHANGE IN SLAB THICKNESS
SCALE: N.T.S.

- GENERAL NOTES
- This Drawing Issue has been checked and approved in accordance with the LOCI Quality Management System.
 - All works shall be carried out in accordance with particular & general specifications, in conjunction with relevant conditions of contract.
 - This drawing shall not be used directly for Construction, but for preparation of Shop Drawings in coordination with other disciplines and Suppliers prior to manufacture, delivery and execution on site.
 - All dimensions and levels are in millimeter, unless noted otherwise, only written dimensions to be followed and not scaled from the drawing.
 - All dimensions to be verified at site and coordinated with other disciplines / manufacturers in the preparation of shop drawings. Any changes shall be validated by the consultant.
 - For elements with indicative design, the contractor / supplier shall submit complete construction details and technical specifications for approval prior to execution. Shop drawings to particularly incorporate details at structural expansion joints as well as expansion / contraction joints needed for the respective materials / finishes / related works.
 - Safety standards and statutory regulations shall be adhered to in the manufacture, supply, storage and installation of all works.
 - Any discrepancy or ambiguity whatsoever with dimensions / details / legends / specifications / etc, shall be brought to the attention of the Consultant and clarification obtained prior to finalization of tender / construction.

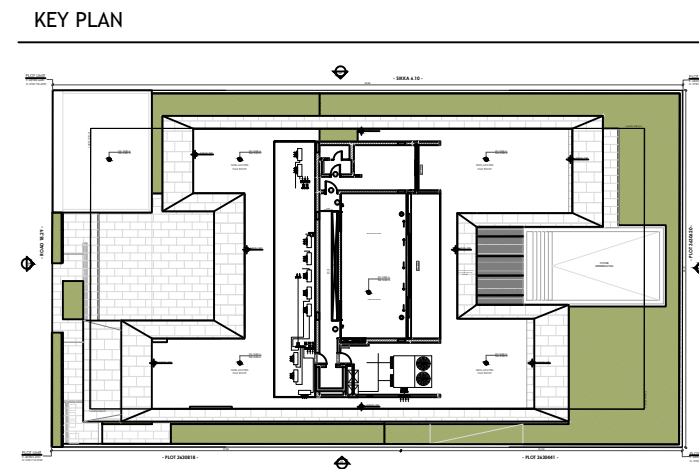

DRAWING REVISIONS				
REV	DATE	DESCRIPTION	CHECKED	APPROVED
00	14.03.2025	ISSUED FOR APPROVAL	AN	BR

CLIENT
TARUN HARISH CHANDRA KHANNA

DRAWING DETAILS
TYPICAL DETAILS - (SHEET 4 OF 10)

SHEET #
269-S-013

REVISION
R0

ISSUE DATE:
14-03-2025

SCALE @ A1
AS SHOWN

PROJECT DETAILS
KHANNA VILLA



PROJECT LOCATION
**PLOT NO. 3630160
Al Manara,
Dubai**

PROJECT PHASE
DETAIL DESIGN

CONSULTANT

LOCI
لوکار

Office M31, KIA Flagship Building
Sheikh Zayed Rd, Al Quoz 1
P. O. Box 72928, Dubai
T +971 4 357 6573
W www.loci.ae