



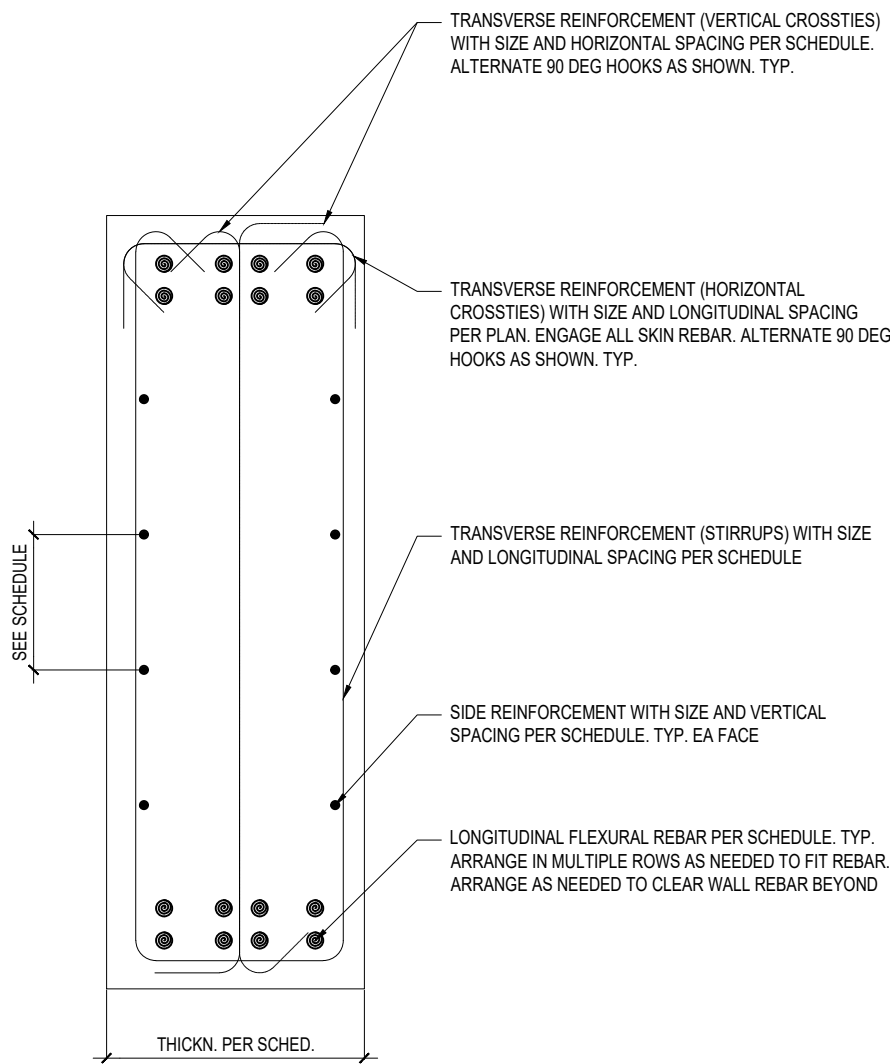

NOTES:


- EXTEND DIAGONAL BAR OR LONGITUDINAL BAR PAST THE OPENING AS NEEDED TO ACHIEVE A DEVELOPMENT LENGTH OF $(1.25 \times L_d)$. IF L_d CANNOT BE ACHIEVED DUE TO PROXIMITY OF REBAR END TO END-OF-WALL, PROVIDE STANDARD HOOK AND EXTEND DIAGONAL BAR OR LONGITUDINAL BAR PAST THE OPENING AS NEEDED TO ACHIEVE A DEVELOPMENT LENGTH OF $(1.25 \times L_d)$. "Ld" AND "Ldh" ARE DETERMINED PER "DEVELOPMENT LENGTH AND SPLICE" DETAIL UNDER CONCRETE TYPICAL DETAILS.
- TRANSVERSE REINFORCEMENT INCLUDES:
 - STIRRUPS
 - CROSSTIES
- VERTICAL LEGS OF TRANSVERSE REINFORCEMENT ARE THE VERTICAL SEGMENTS OF STIRRUPS (2-VERTICAL LEGS FOR EACH STIRRUP) AND VERTICAL CROSSTIES (ONE VERTICAL LEG FOR EACH VERTICAL CROSSTIE).

B2 SECTION

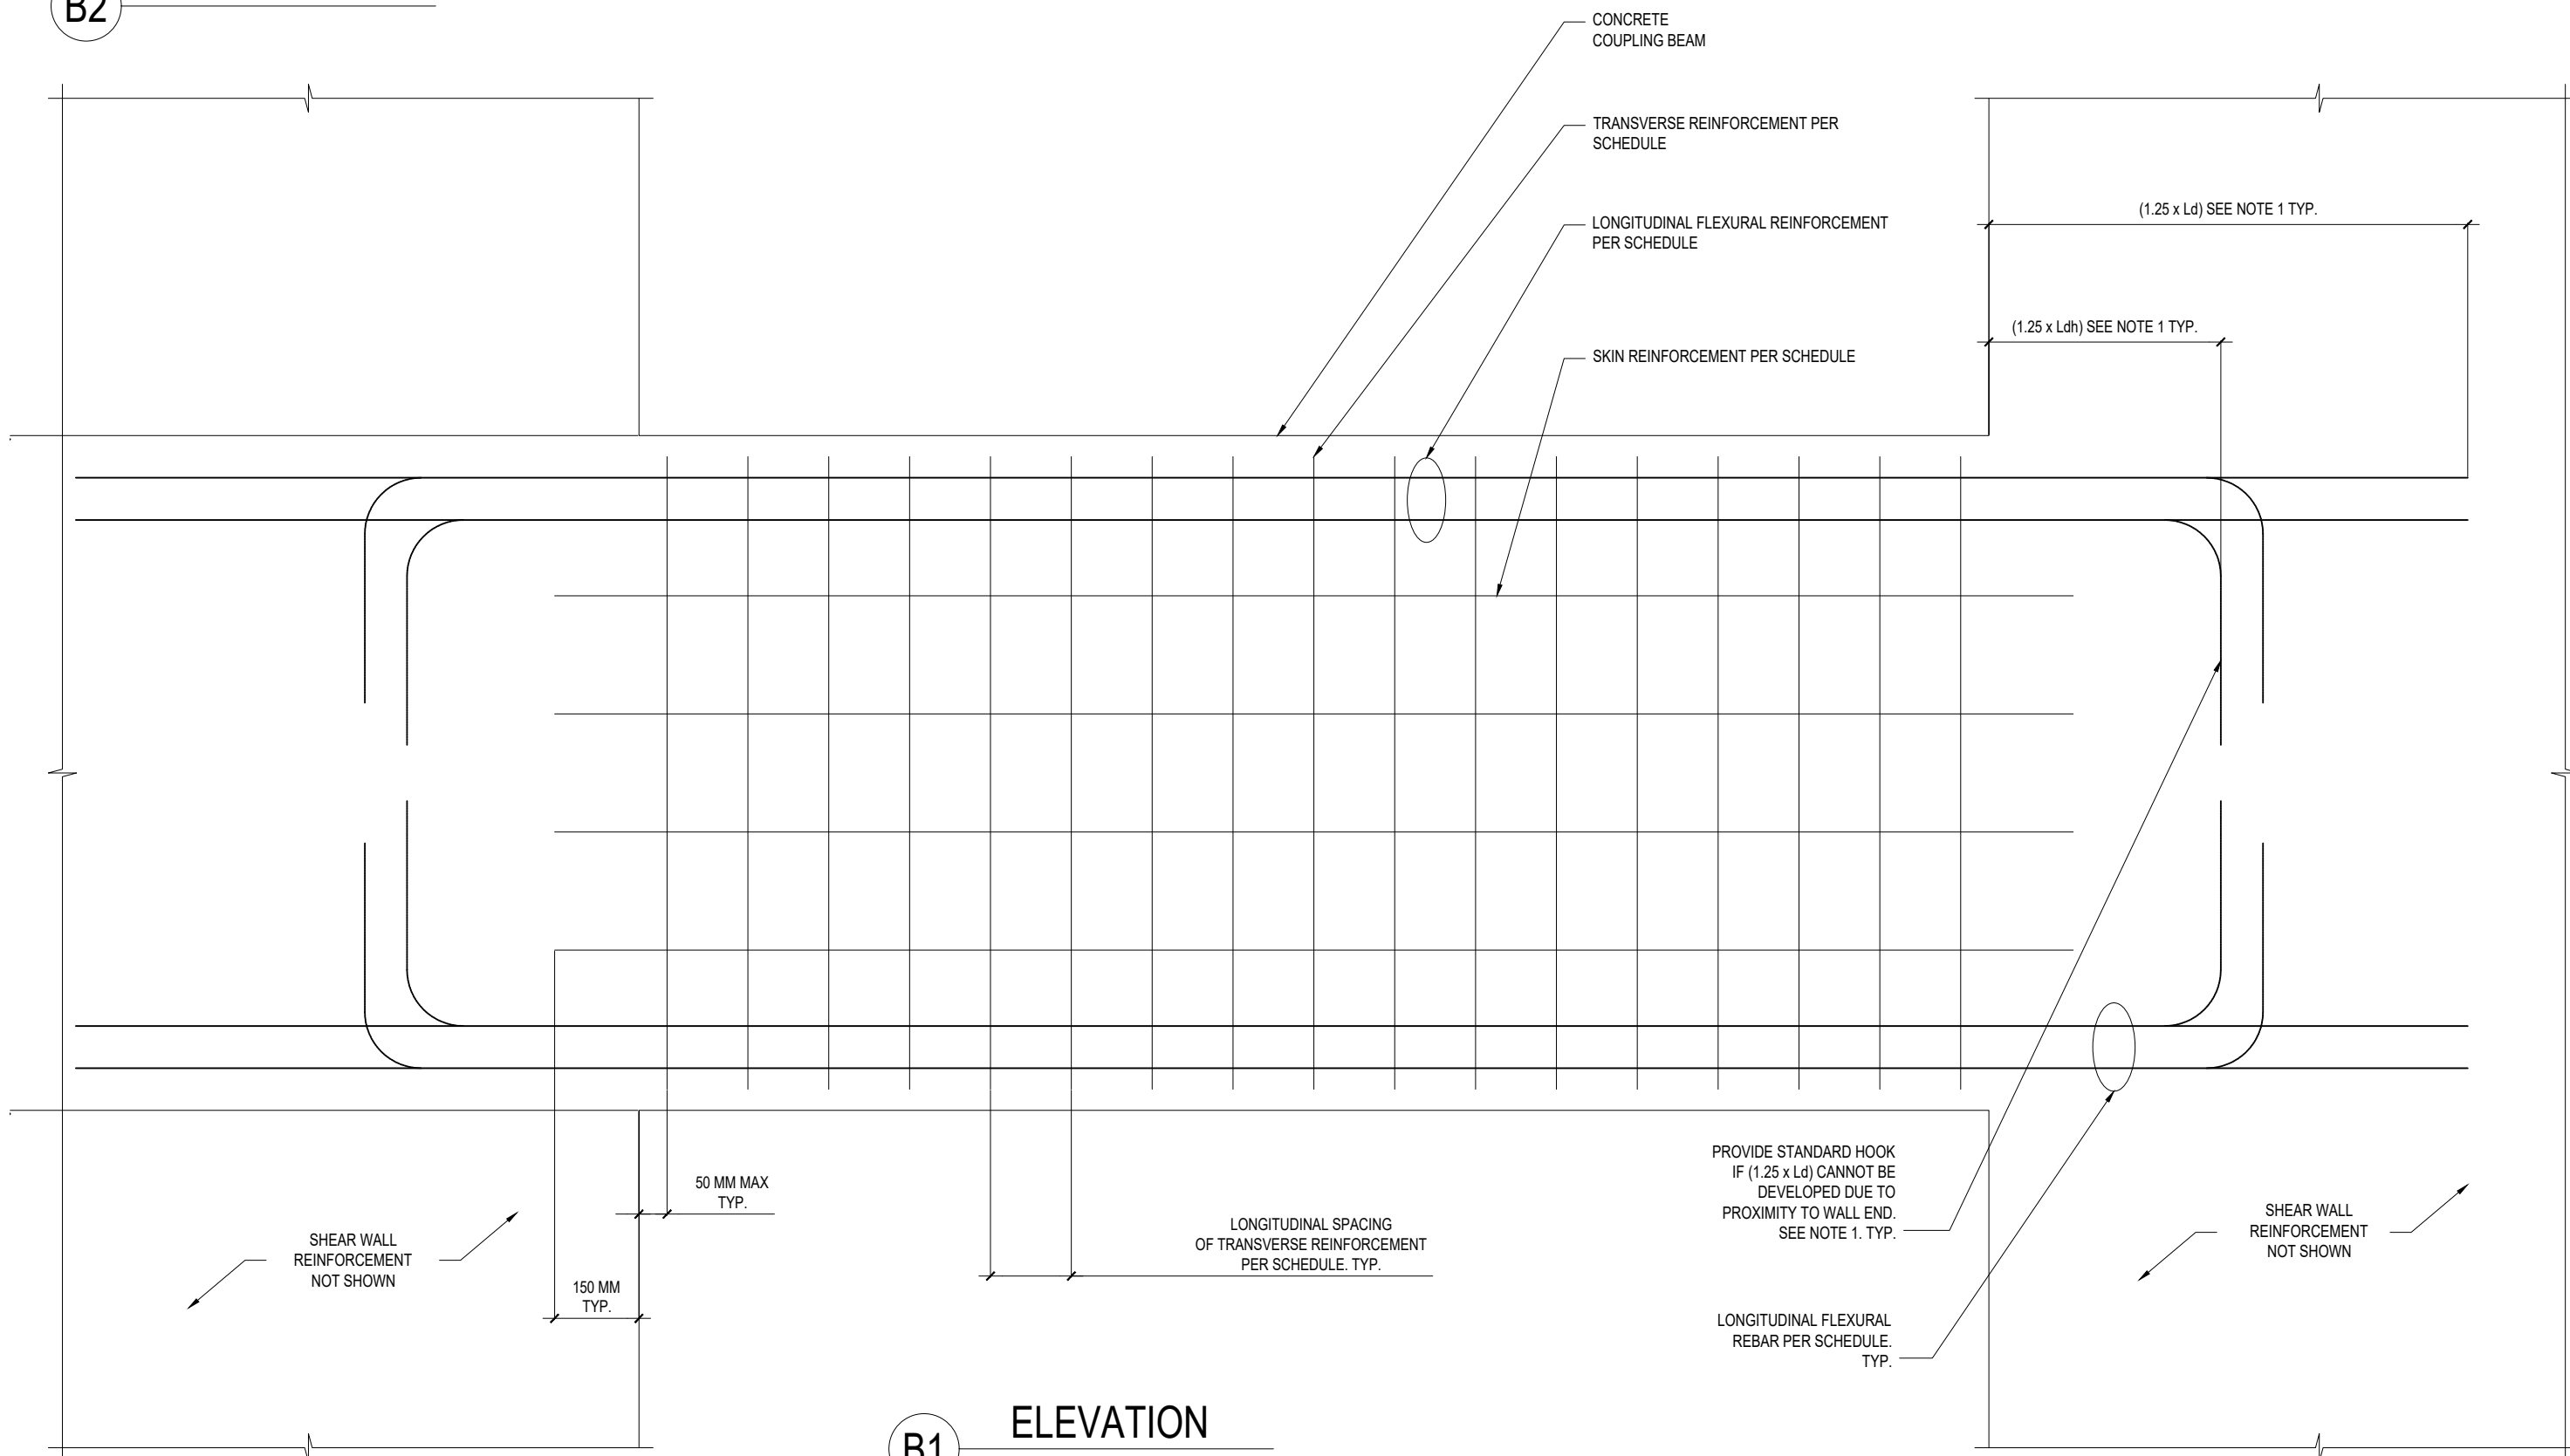


B1 ELEVATION



COUPLING BEAM TYPICAL DETAIL
SCALE: N.T.S.

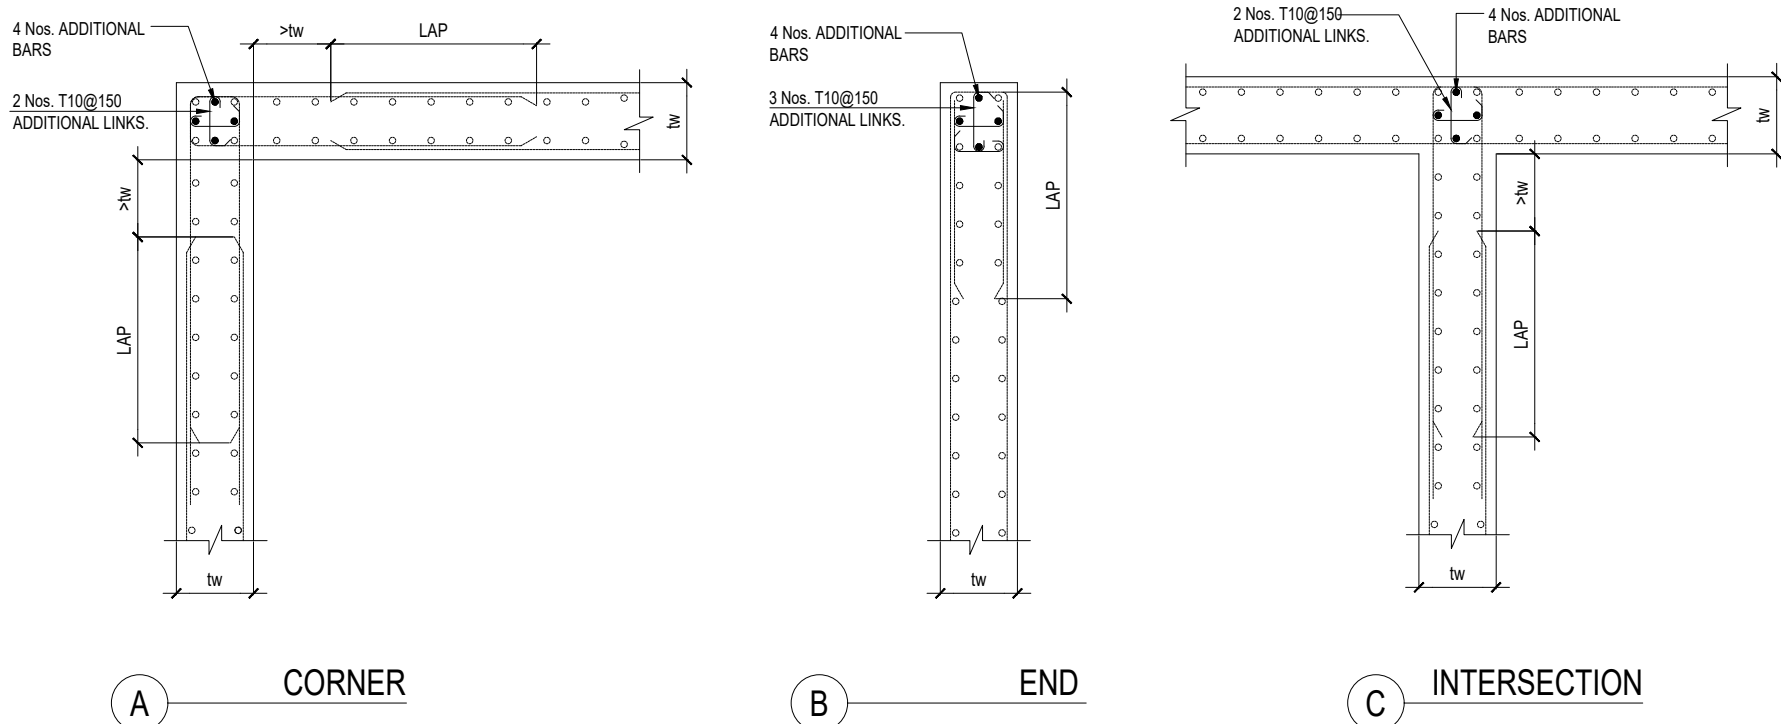

TYPICAL WALL JUNCTION DETAILS
SCALE: N.T.S.

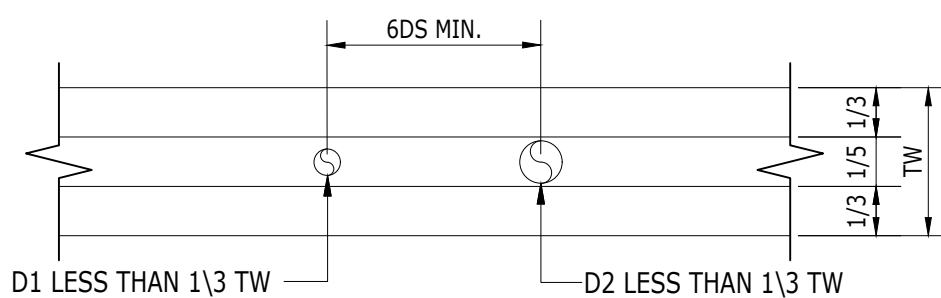


CONDUIT PLACEMENT IN WALLS
SCALE: N.T.S.

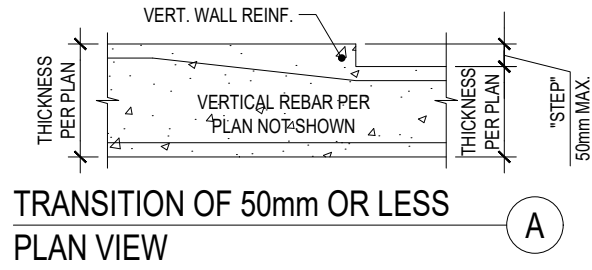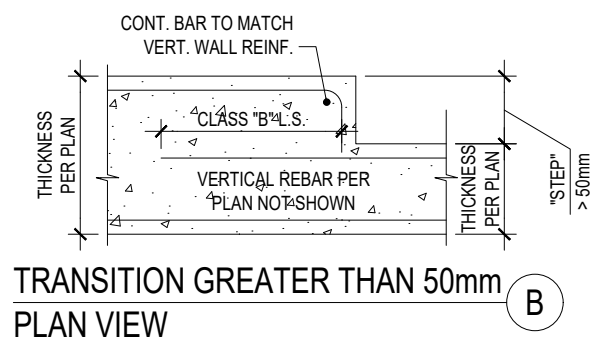

NOTES:

- FOR LOCATION OF TRANSITION IN WALL THICKNESS, SEE PLAN.
- THIS DETAIL APPLIES WHERE DIFFERENT WALL THICKNESS IS SPECIFIED ALONG THE LENGTH OF THE WALL.
- UNLESS NOTED OTHERWISE, FOR BASEMENT RETAINING WALLS, THE OUTSIDE/EARTHRETAINED FACE SHALL BE CONTINUOUS AND THE TRANSITION OCCURS ON THE INSIDE FACE.
- REFER TO PLAN FOR OUTER & INNER REBAR ORIENTATION.


WALL THICKNESS TRANSITION
SCALE: N.T.S.

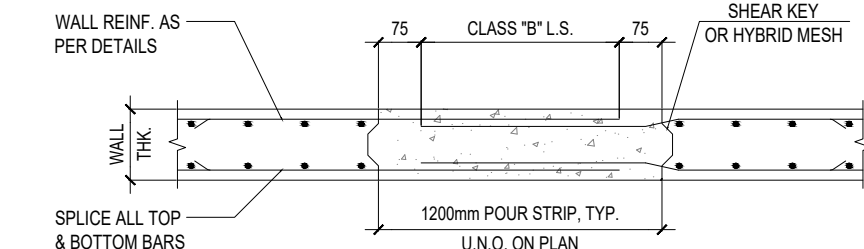


NOTES:

- RETAIN SHORING UNTIL POUR STRIP CONCRETE REACHES SLAB'S DESIGN STRENGTH (14 DAYS MIN.)
- CLOSURE STRIP TO BE POURED WITH LOW-SHRINK CONCRETE NOT LESS THAN 60 DAYS AFTER STRESSING, U.N.O.
- SHRINKAGE STRIPS EXTENDED INTO ADJACENT R.C. SLABS.
- ROUGHEN & CLEAN JOINTS & WET PRIOR TO PLACING CONCRETE


5 TYP. POUR STRIP IN R.C. WALL DETAIL
SCALE: N.T.S.

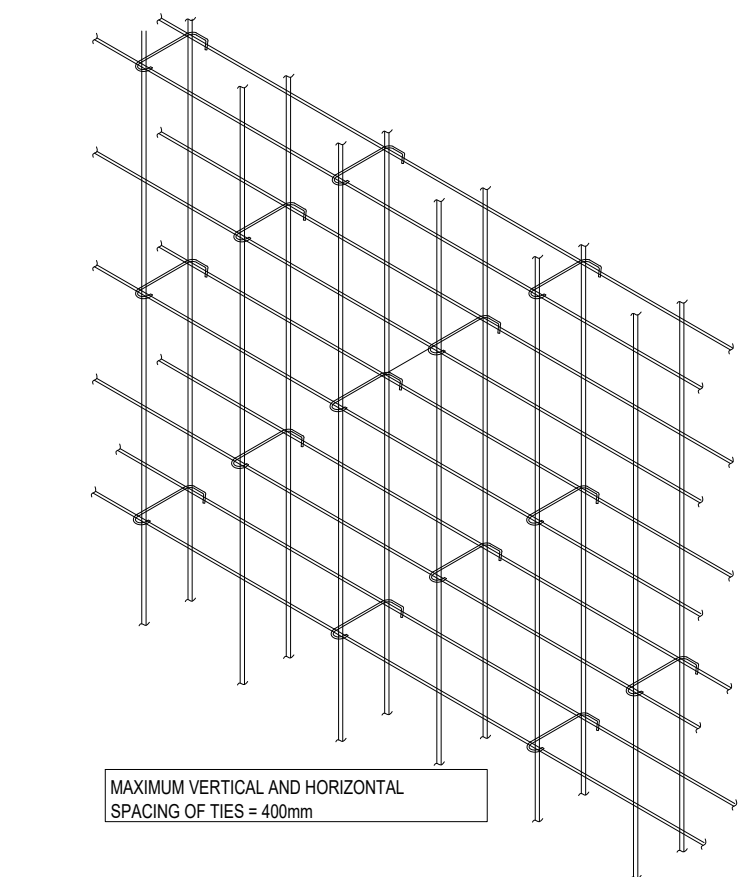


6 TYPICAL STAGGERED TIES IN WALLS
SCALE: N.T.S.

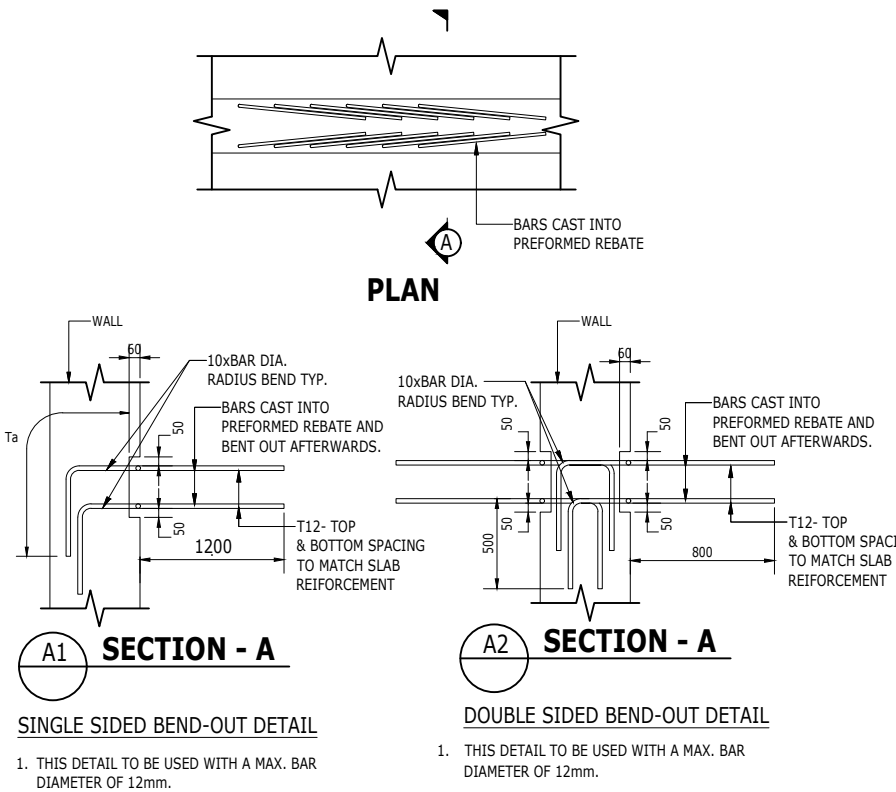

7 BEND-OUT DETAIL
SCALE: N.T.S.

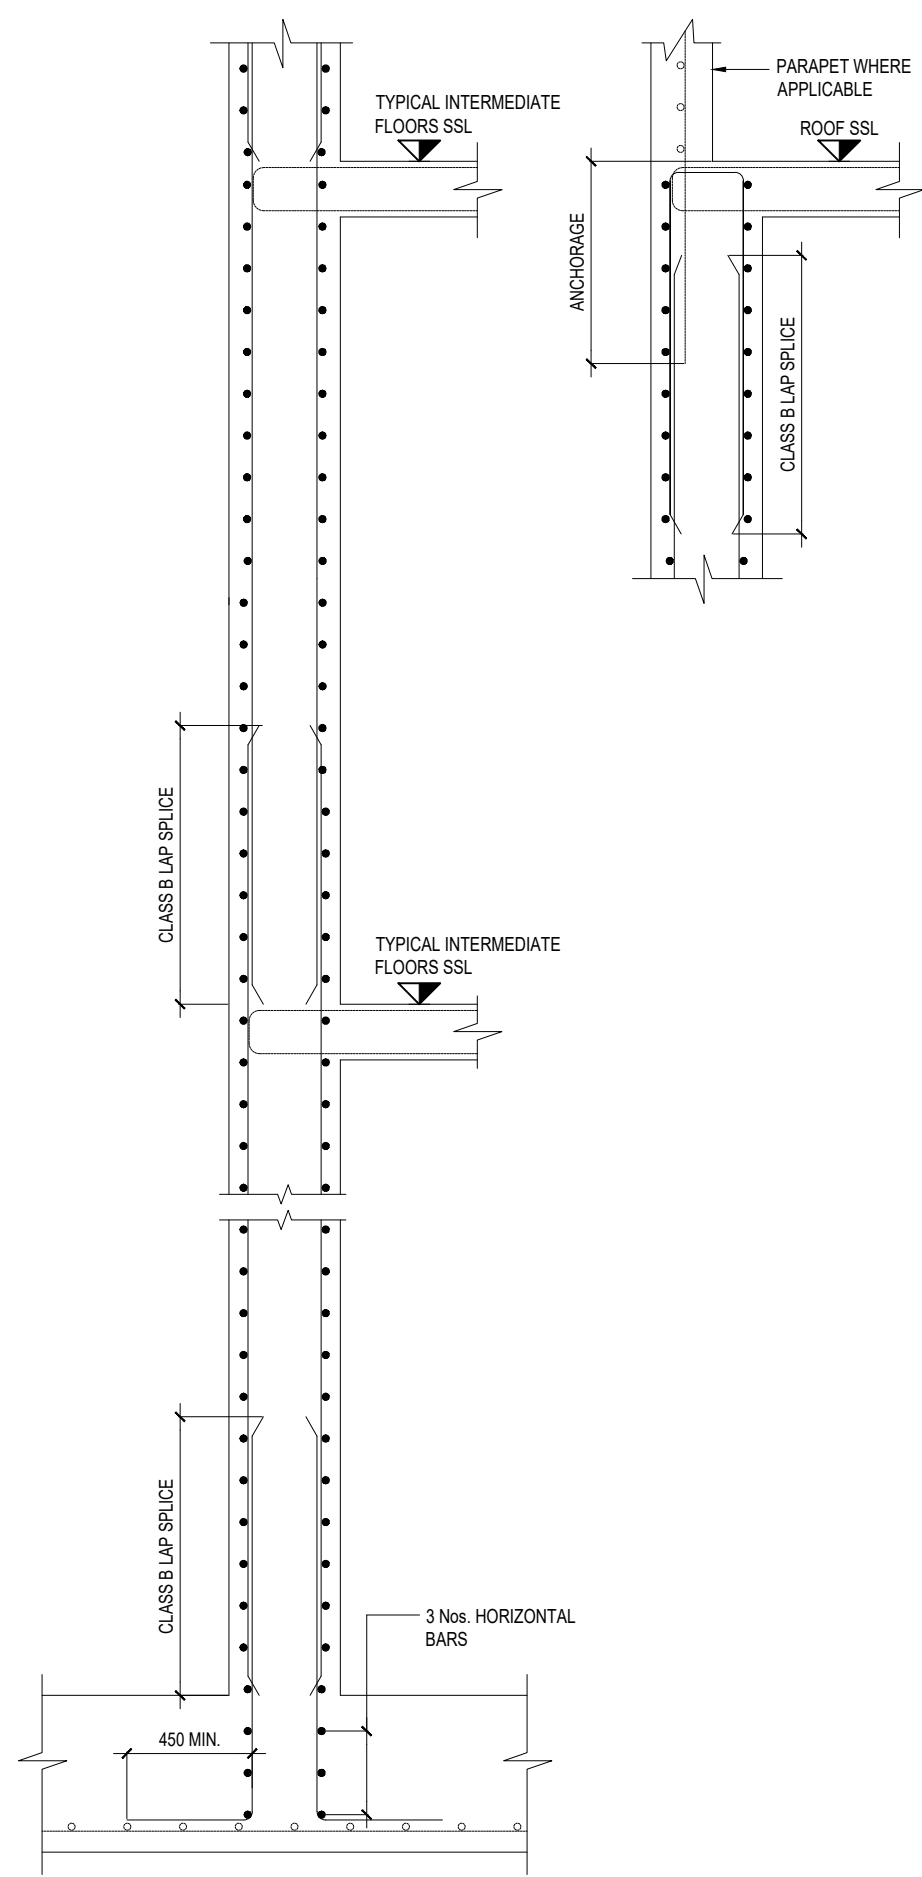

8 TYPICAL SHEAR WALL SECTION
SCALE: N.T.S.

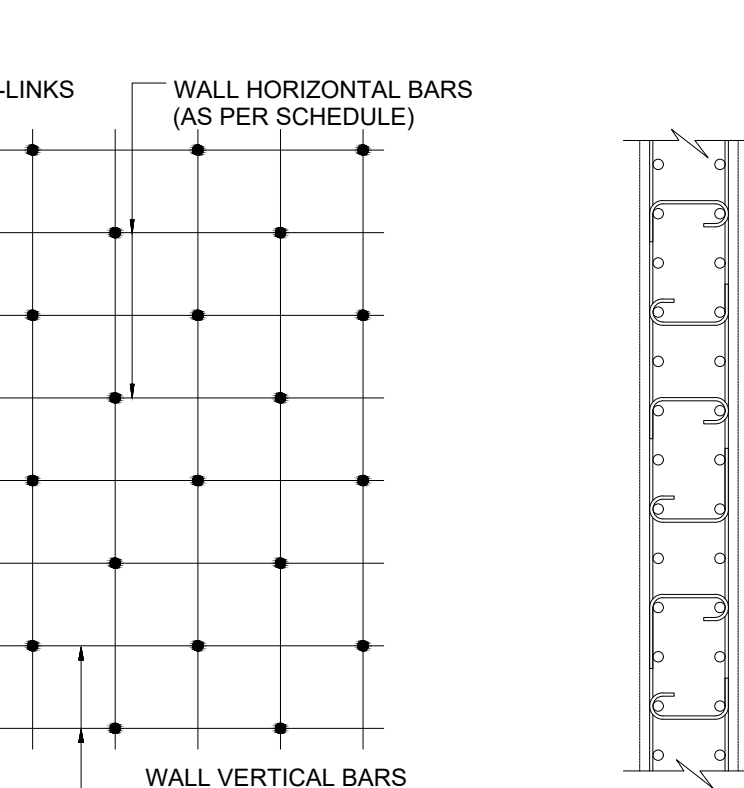


9 PIPE PENETRATION THROUGH WALL
SCALE: N.T.S.

GENERAL NOTES

- This Drawing Issue has been checked and approved in accordance with the LOCI Quality Management System.
- All works shall be carried out in accordance with particular B general specifications, in conjunction with relevant conditions of contract.
- This drawing shall not be used directly for Construction, but for preparation of Shop Drawings in coordination with other disciplines and Suppliers prior to manufacture, delivery and execution on site.
- All dimensions and levels are in millimeter, unless noted otherwise. Only written dimensions to be followed and not scaled from the drawing.
- All dimensions to be verified at site and coordinated with other disciplines/ manufacturers in the preparation of shop drawings. Any changes shall be validated by the consultant.
- For elements with indicative design, the contractor / supplier shall submit complete construction details and technical specifications for approval prior to execution. Shop drawings to particularly incorporate details at structural expansion joints as well as expansion / construction joints needed for the respective materials/ finishes / related works.
- Safety standards and statutory regulations shall be adhered to in the manufacture, supply, storage and installation of all works.
- Any discrepancy or ambiguity whatsoever with dimensions / details / legends / specifications / etc, shall be brought to the attention of the Consultant and clarification obtained prior to finalization of tender / construction.

KEY PLAN

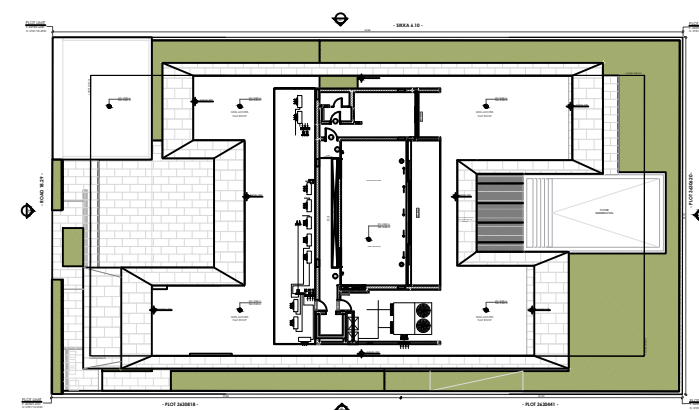

DRAWING REVISIONS

REV	DATE	DESCRIPTION	CHECKED	APPROVED
00	14-03-2025	ISSUED FOR APPROVAL	AN	BR

CLIENT

TARUN HARISH CHANDRA KHANNA

DRAWING DETAILS

TYPICAL DETAILS - (SHEET 8 OF 10)

SHEET

269-S-017

REVISION

R0

ISSUE DATE:

14-03-2025

SCALE @ A1

AS SHOWN

PROJECT DETAILS

KHANNA VILLA



PROJECT LOCATION

PLOT NO. 3630160
Al Manara,
Dubai

PROJECT NUMBER

269

PROJECT PHASE

DETAIL DESIGN

CONSULTANT

LOCI
لوکار

Office M31, KIA Flagship
Building
Sheikh Zayed Rd, Al Quoz 1
P. O. Box 72928, Dubai
T +971 4 357 6573
W www.loci.ae