


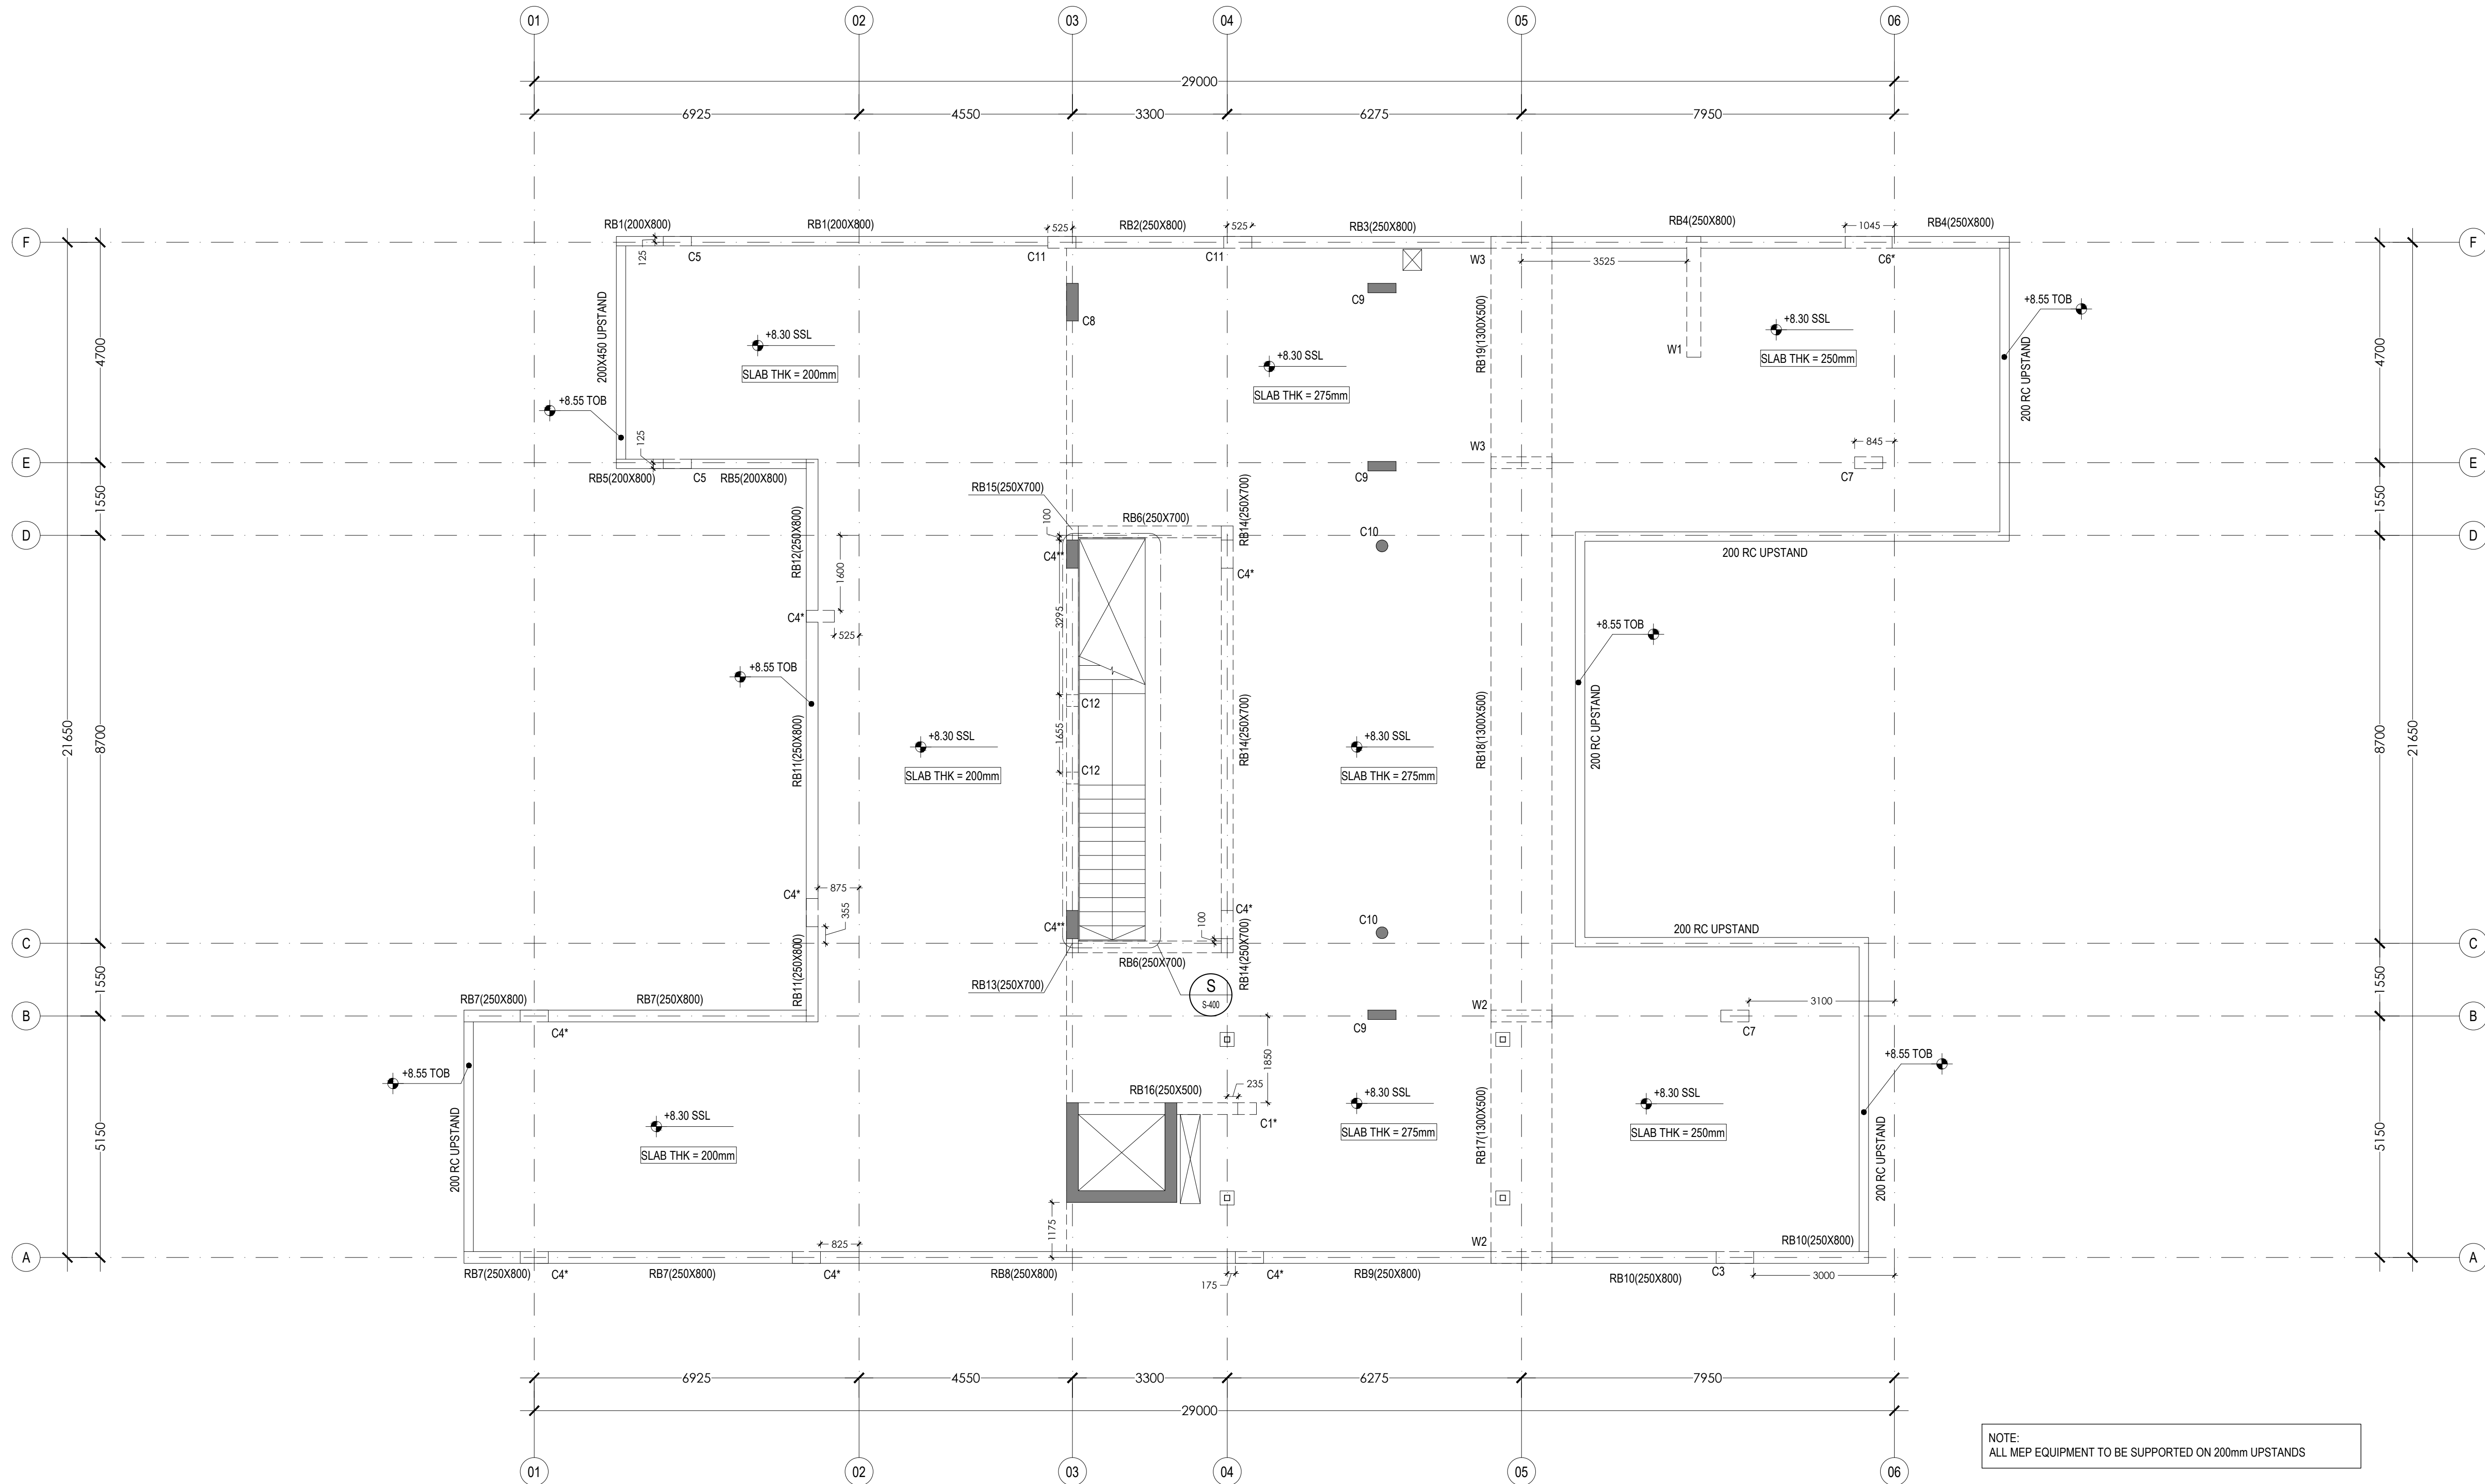


NOTE:
ALL MEP EQUIPMENT TO BE SUPPORTED ON 200mm UPSTANDS

LEGEND	
	CONCRETE COLUMN PER SCHEDULE/S-201
	CONCRETE WALL PER SCHEDULE/S-202
	CONCRETE COLUMN/WALL BELOW
	CONCRETE BEAM PER SCHEDULE/S-200
	OPENING IN SLAB
	LIGHTWEIGHT INFILL
	CHANGE IN SLAB LEVEL
	STRUCTURAL SLAB LEVEL
	TOP OF BEAM/UPSTAND LEVEL

1 ROOF FLOOR GENERAL ARRANGEMENT PLAN
SCALE: 1:75

GENERAL NOTES

- This Drawing Issue has been checked and approved in accordance with the LOCI Quality Management System.
- All works shall be carried out in accordance with particular & general specifications, in conjunction with relevant conditions of contract.
- This drawing shall not be used directly for Construction, but for preparation of Shop Drawings in coordination with other disciplines and Suppliers prior to manufacture, delivery and execution on site.
- All dimensions and levels are in millimeter, unless noted otherwise, only written dimensions to be followed and not scaled from the drawing.
- All dimensions to be verified at site and coordinated with other disciplines/ manufacturers in the preparation of shop drawings. Any changes shall be validated by the consultant.
- For elements with indicative design, the contractor / supplier shall submit complete construction details and technical specifications for approval prior to execution. Shop drawings to particularly incorporate details at structural expansion joints as well as expansion / construction joints needed for the respective materials/ finishes / related works.
- Safety standards and statutory regulations shall be adhered to in the manufacture, supply, storage and installation of all works.
- Any discrepancy or ambiguity whatsoever with dimensions / details / legends / specifications / etc, shall be brought to the attention of the Consultant and clarification obtained prior to finalization of tender / construction.

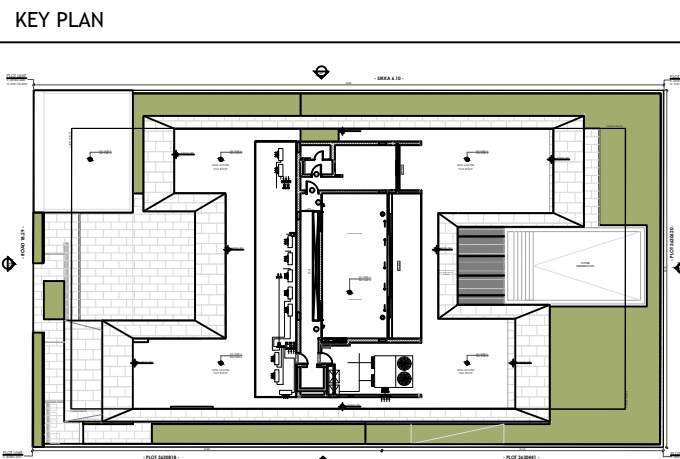

DRAWING REVISIONS				
REV	DATE	DESCRIPTION	CHECKED	APPROVED
00	14.03.2025	ISSUED FOR APPROVAL	AN	BR

CLIENT
TARUN HARISH CHANDRA KHANNA

DRAWING DETAILS
ROOF FLOOR
GENERAL ARRANGEMENT PLAN
SHEET #
269-S-103-A
REVISION
R0
ISSUE DATE:
14-03-2025
SCALE @ A1
AS SHOWN



PROJECT LOCATION
PLOT NO. 3630160
Al Manara,
Dubai
PROJECT NUMBER
269

PROJECT PHASE
DETAIL DESIGN

CONSULTANT
LOCI
لوکار
Office M31, KIA Flagship
Building
Sheikh Zayed Rd, Al Quoz 1
P. O. Box 72928, Dubai
T +971 4 357 6573
W www.loci.ae