




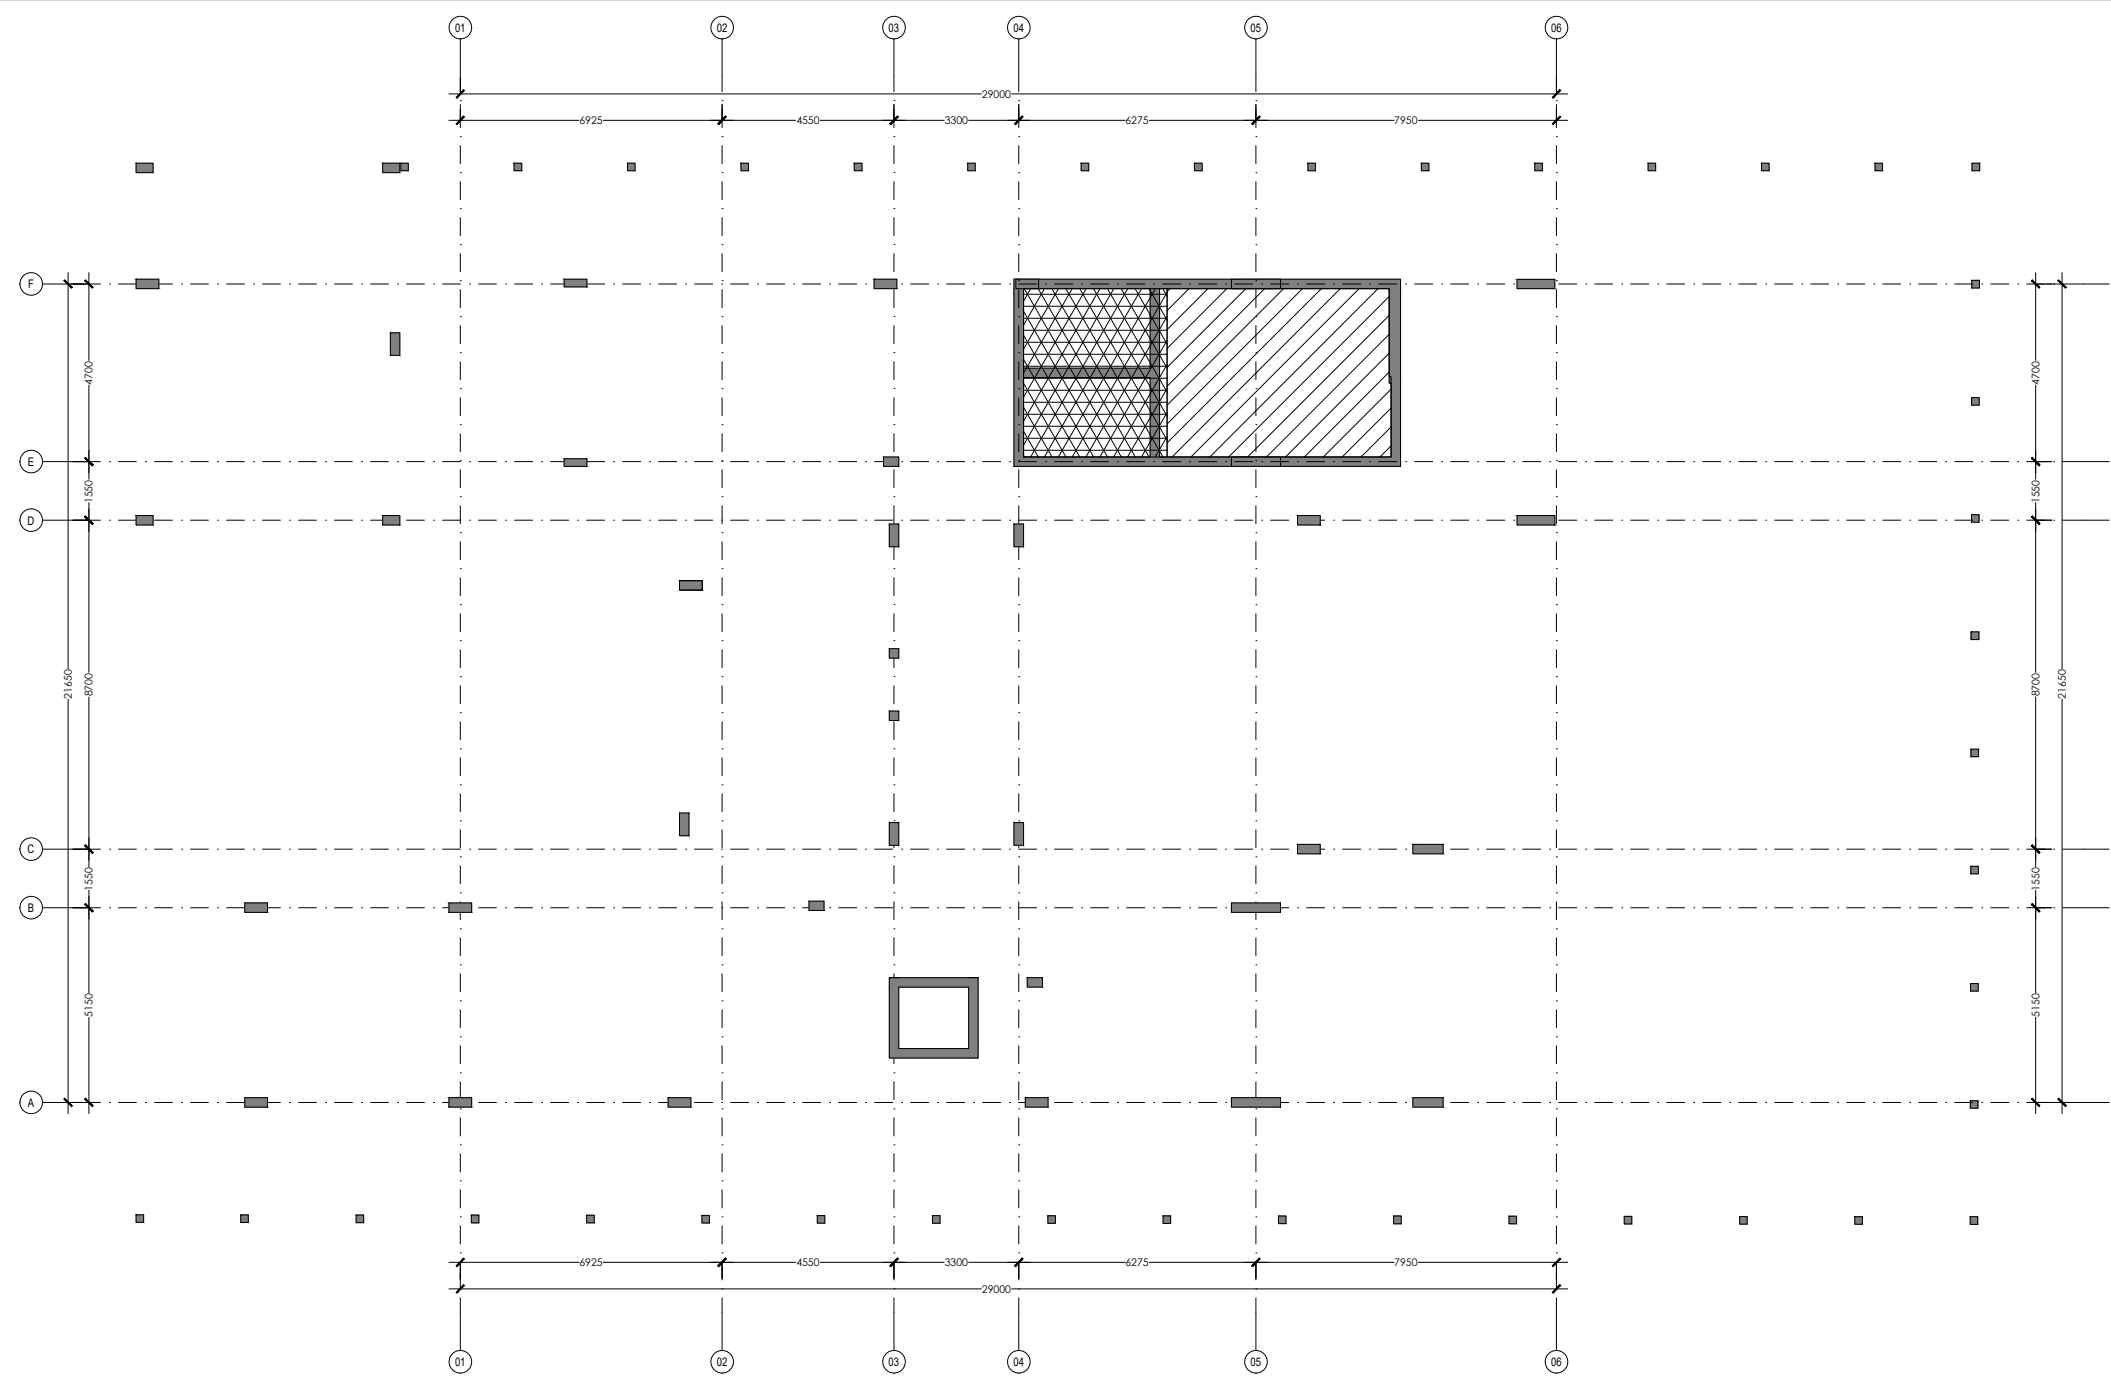


BASEMENT FLOOR LOADING PLAN
SCALE: 1:250

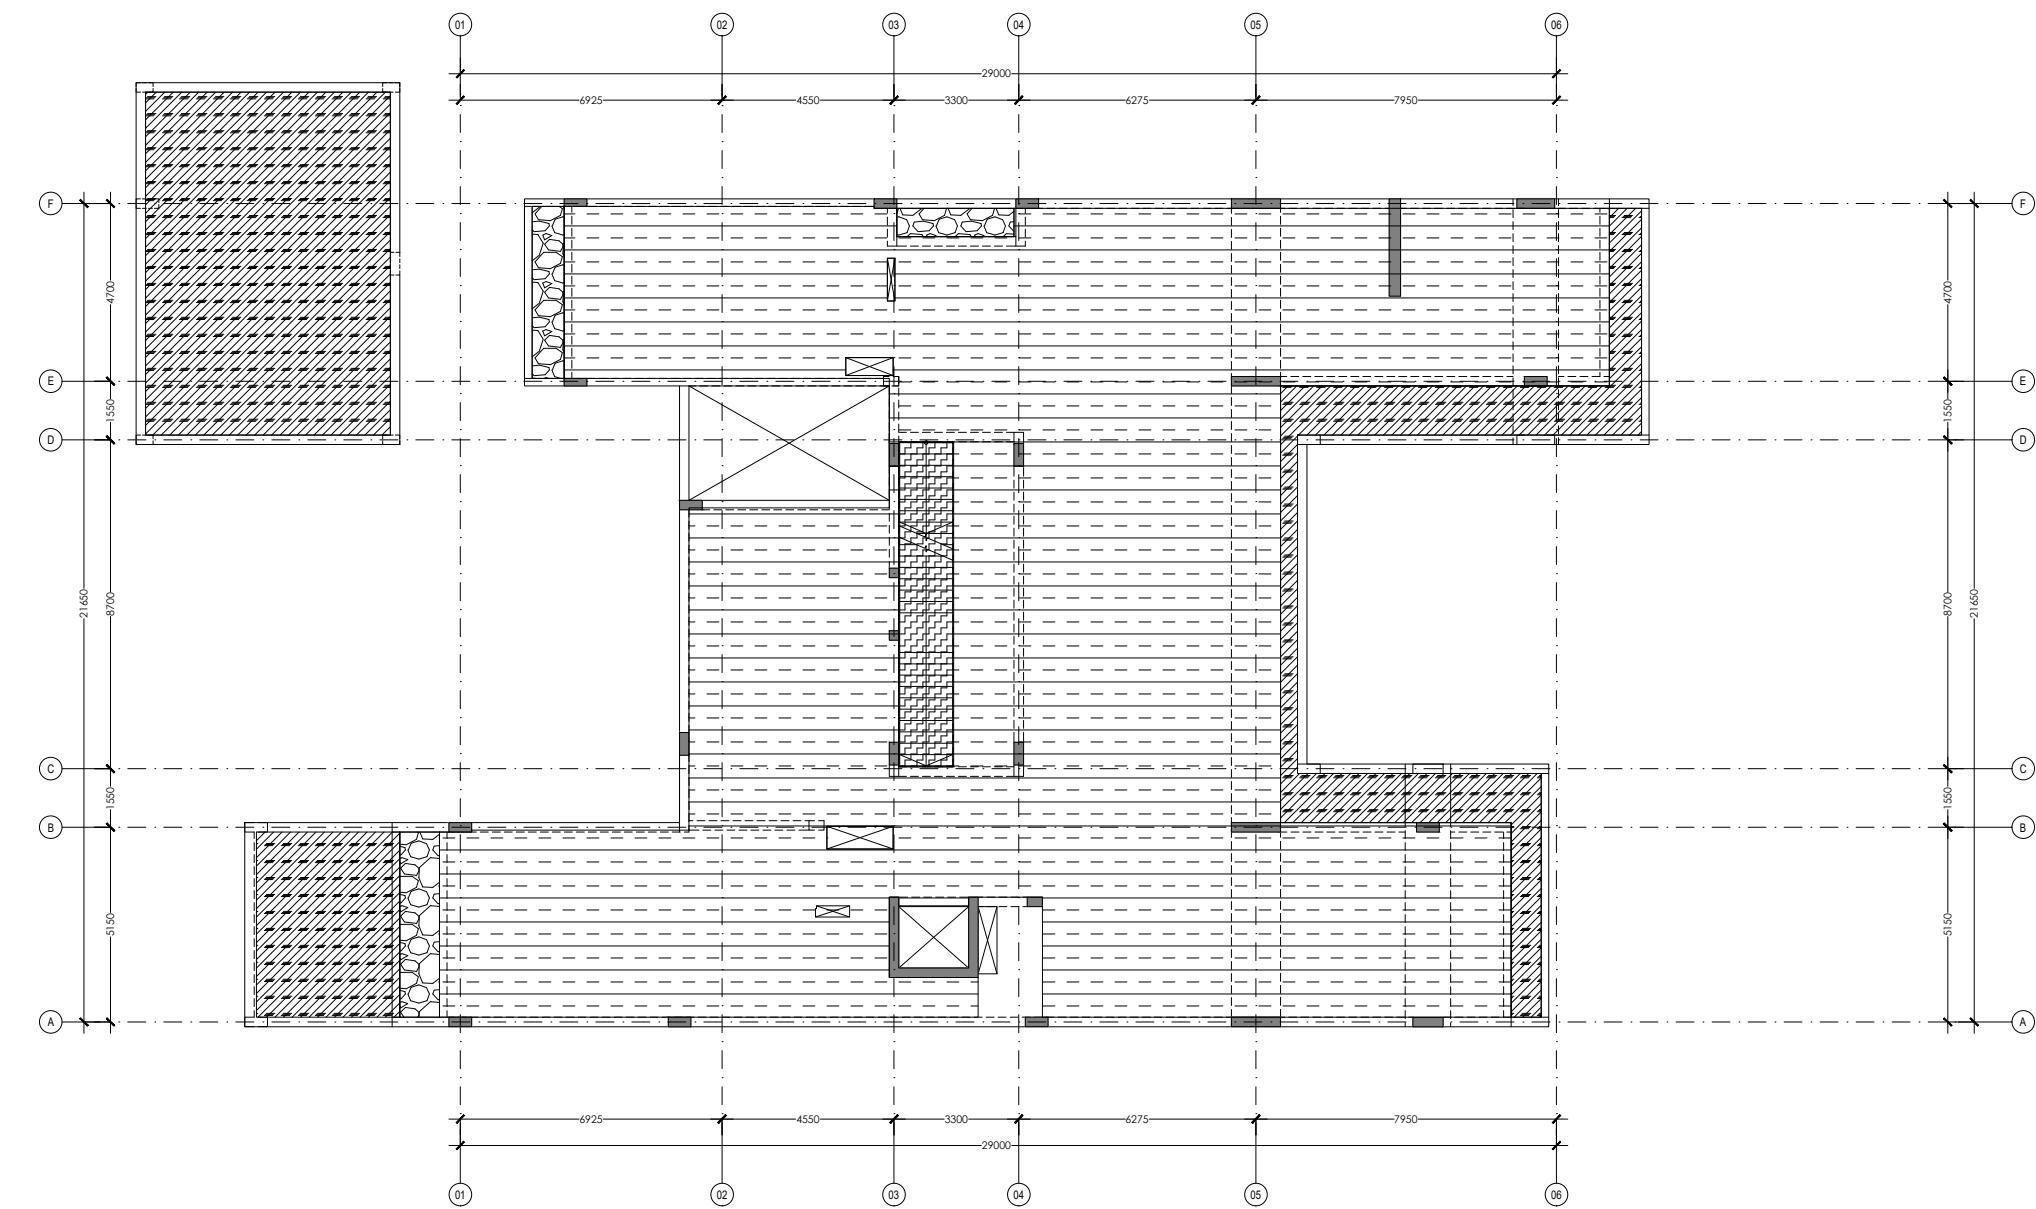


FIRST FLOOR LOADING PLAN
SCALE: 1:250

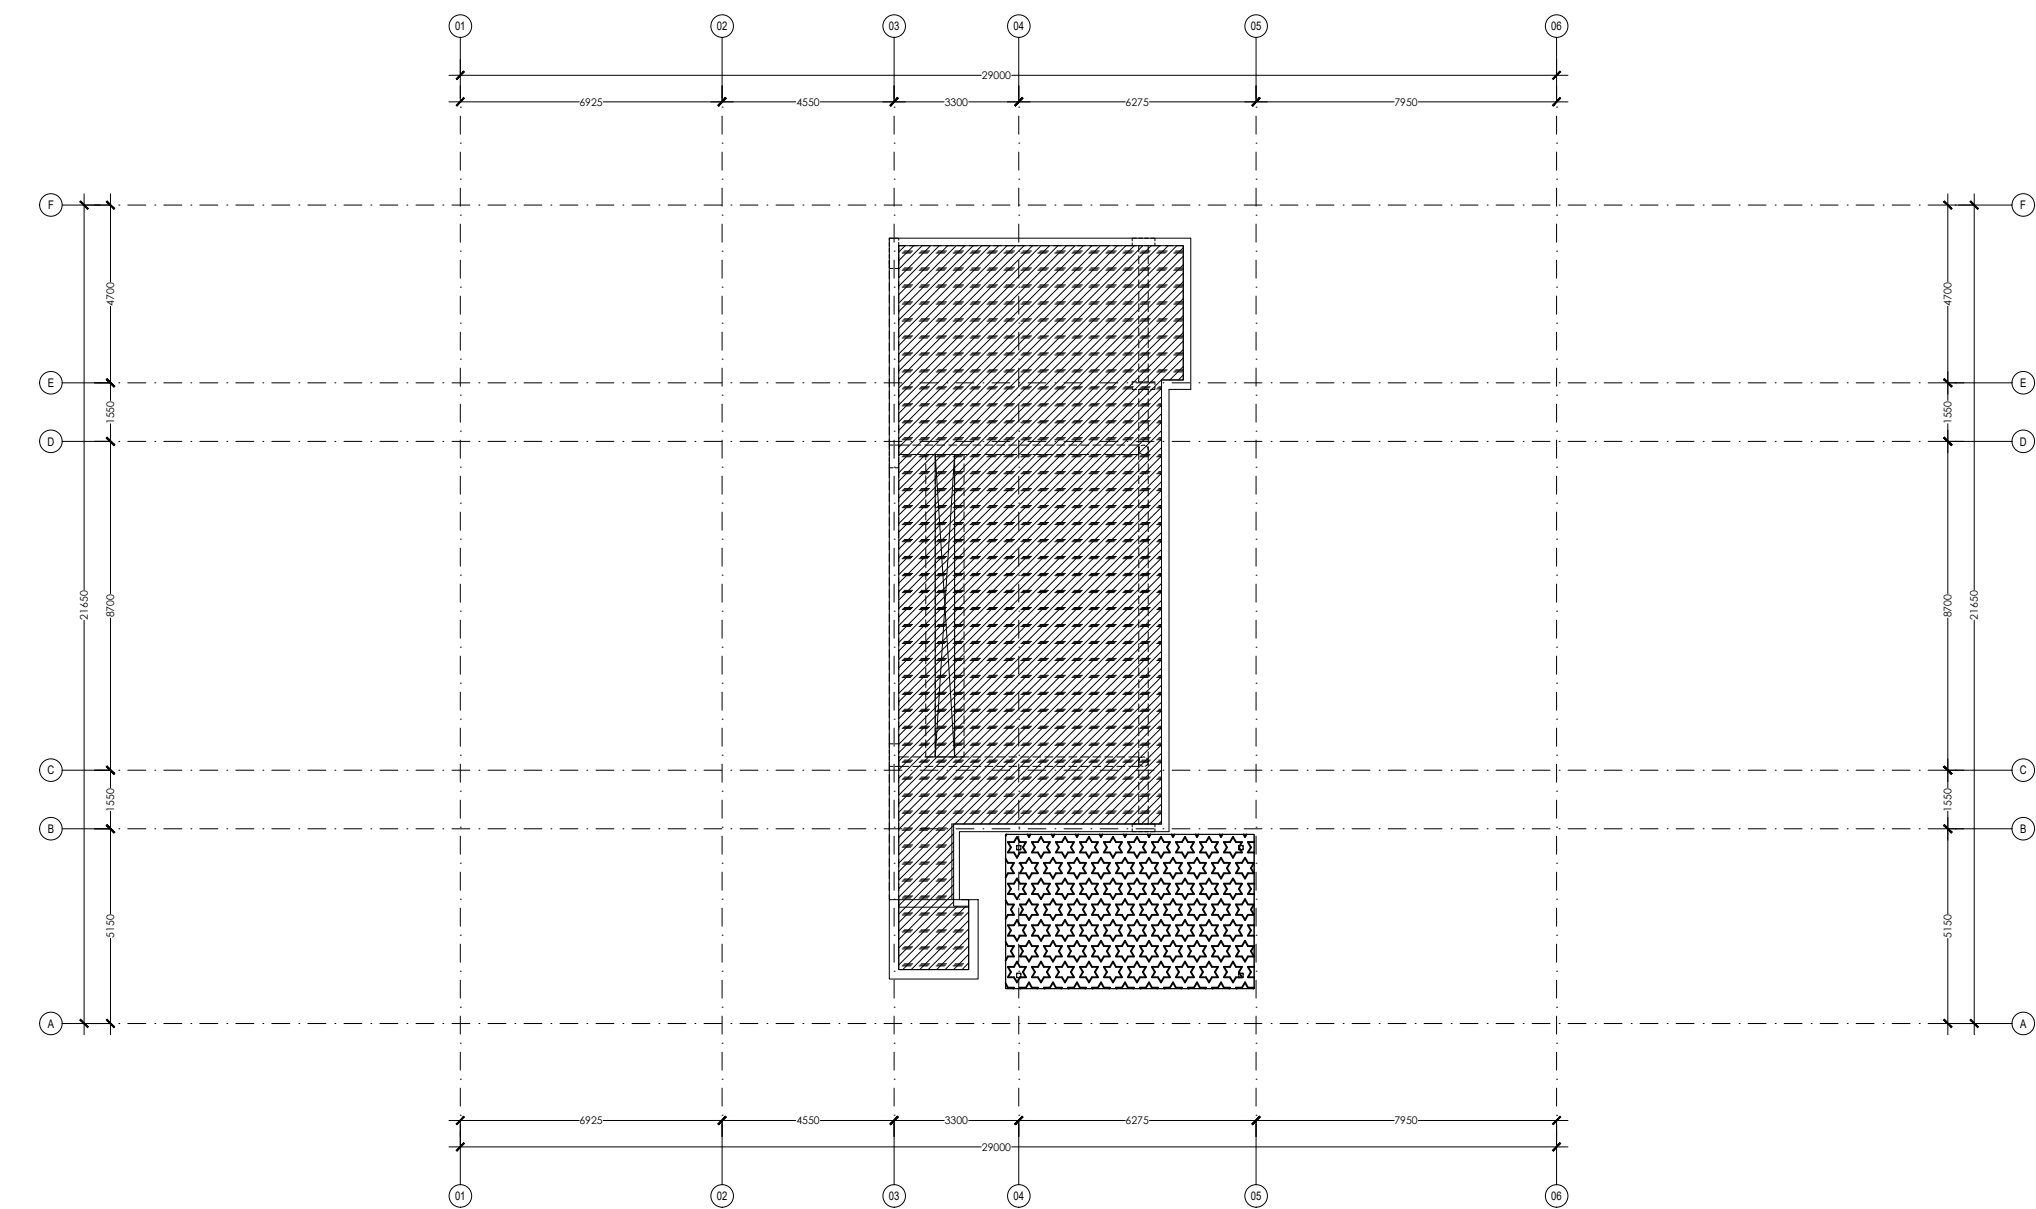

UPPER ROOF FLOOR LOADING PLAN
SCALE: 1:250

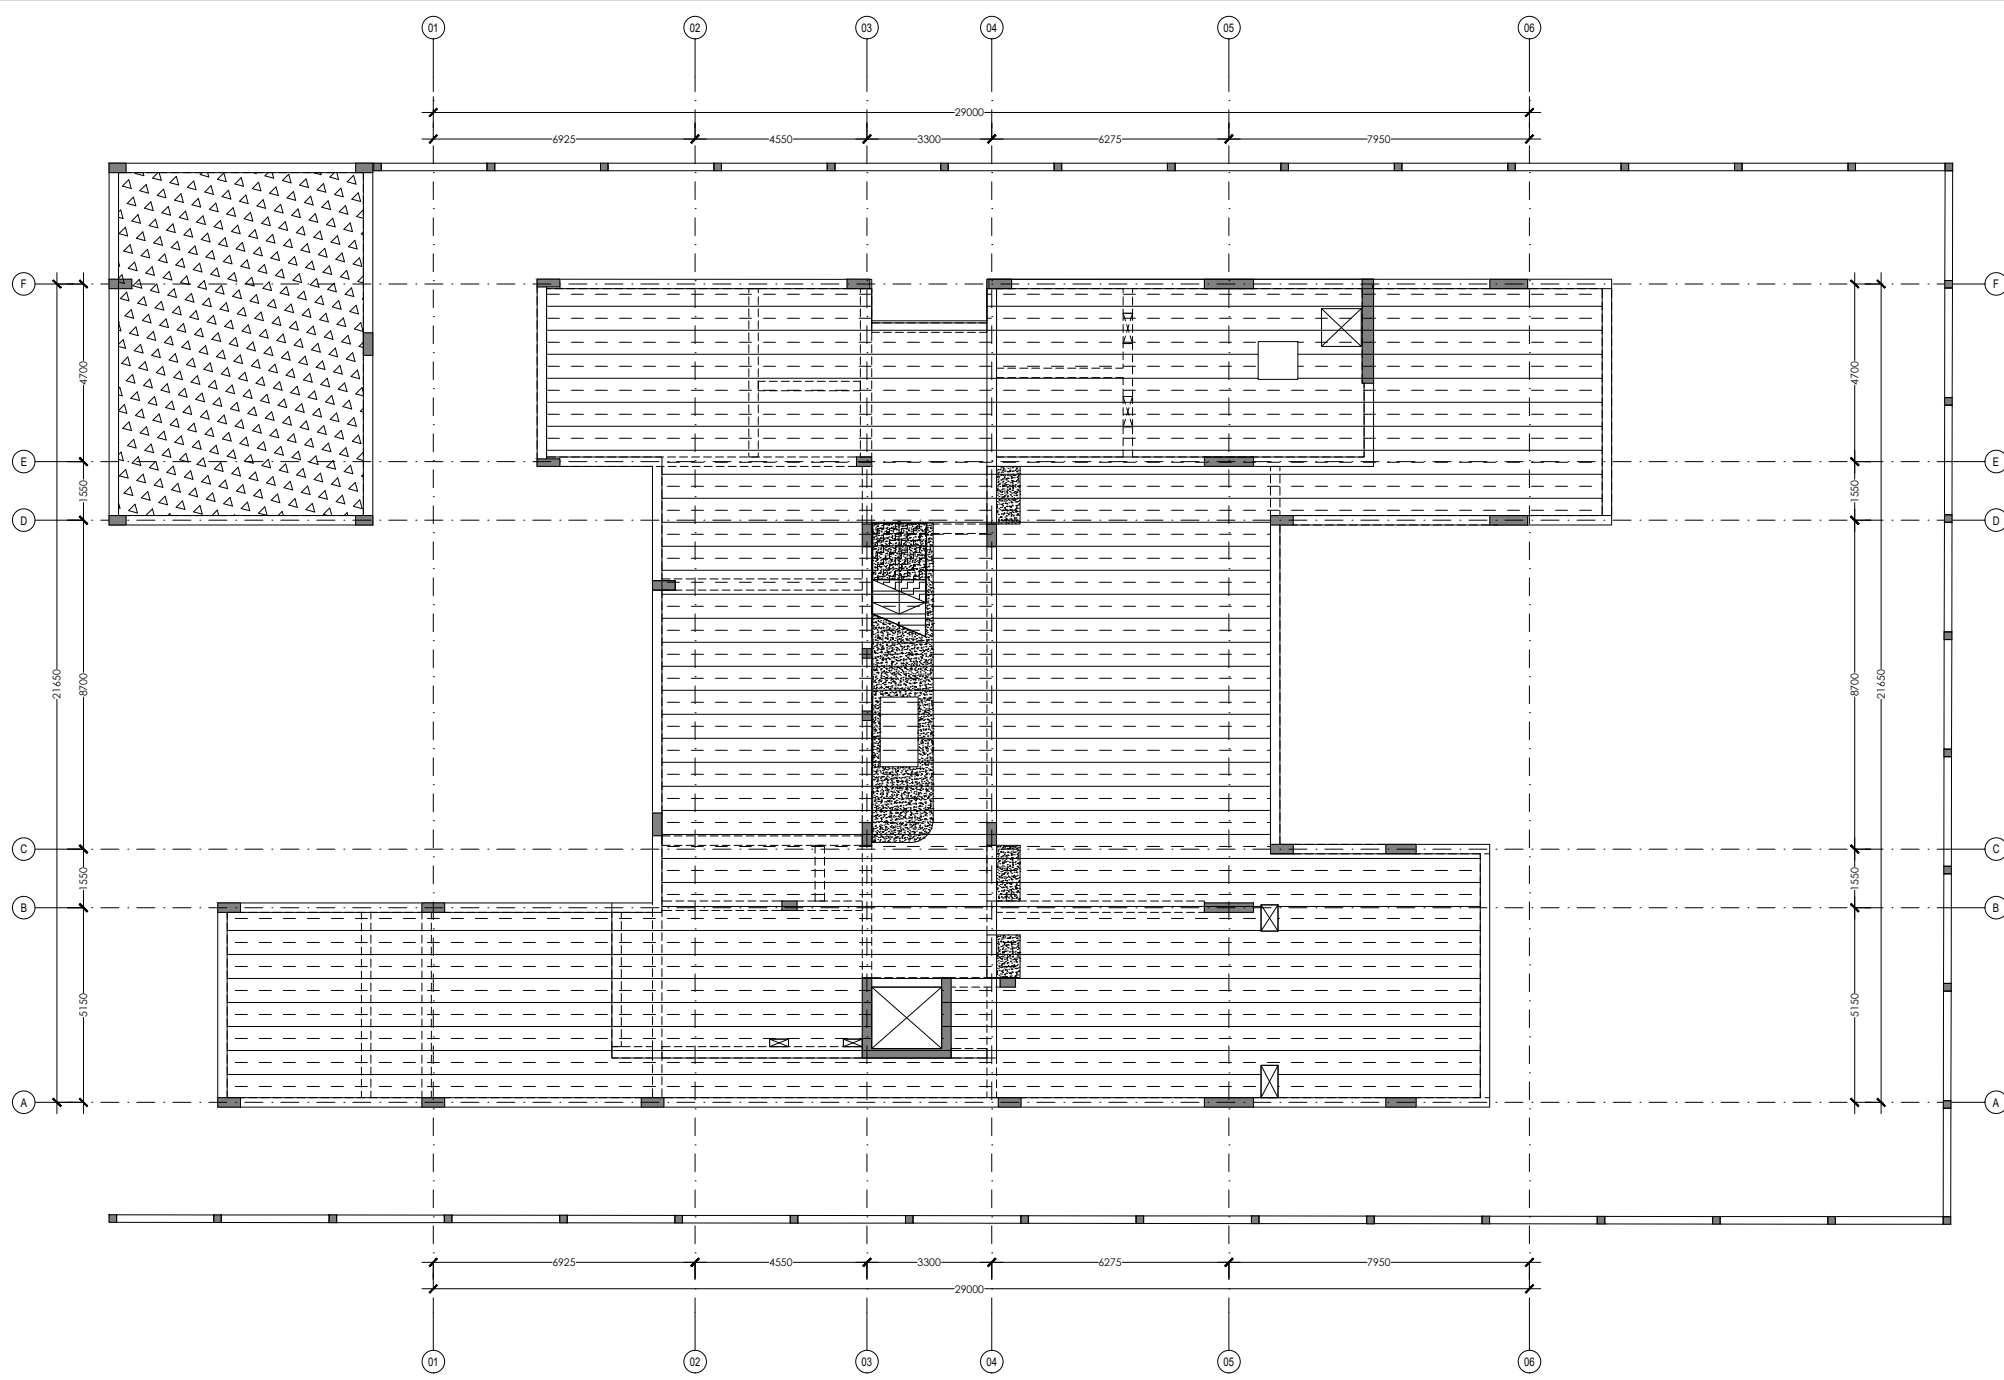

GROUND FLOOR LOADING PLAN
SCALE: 1:250

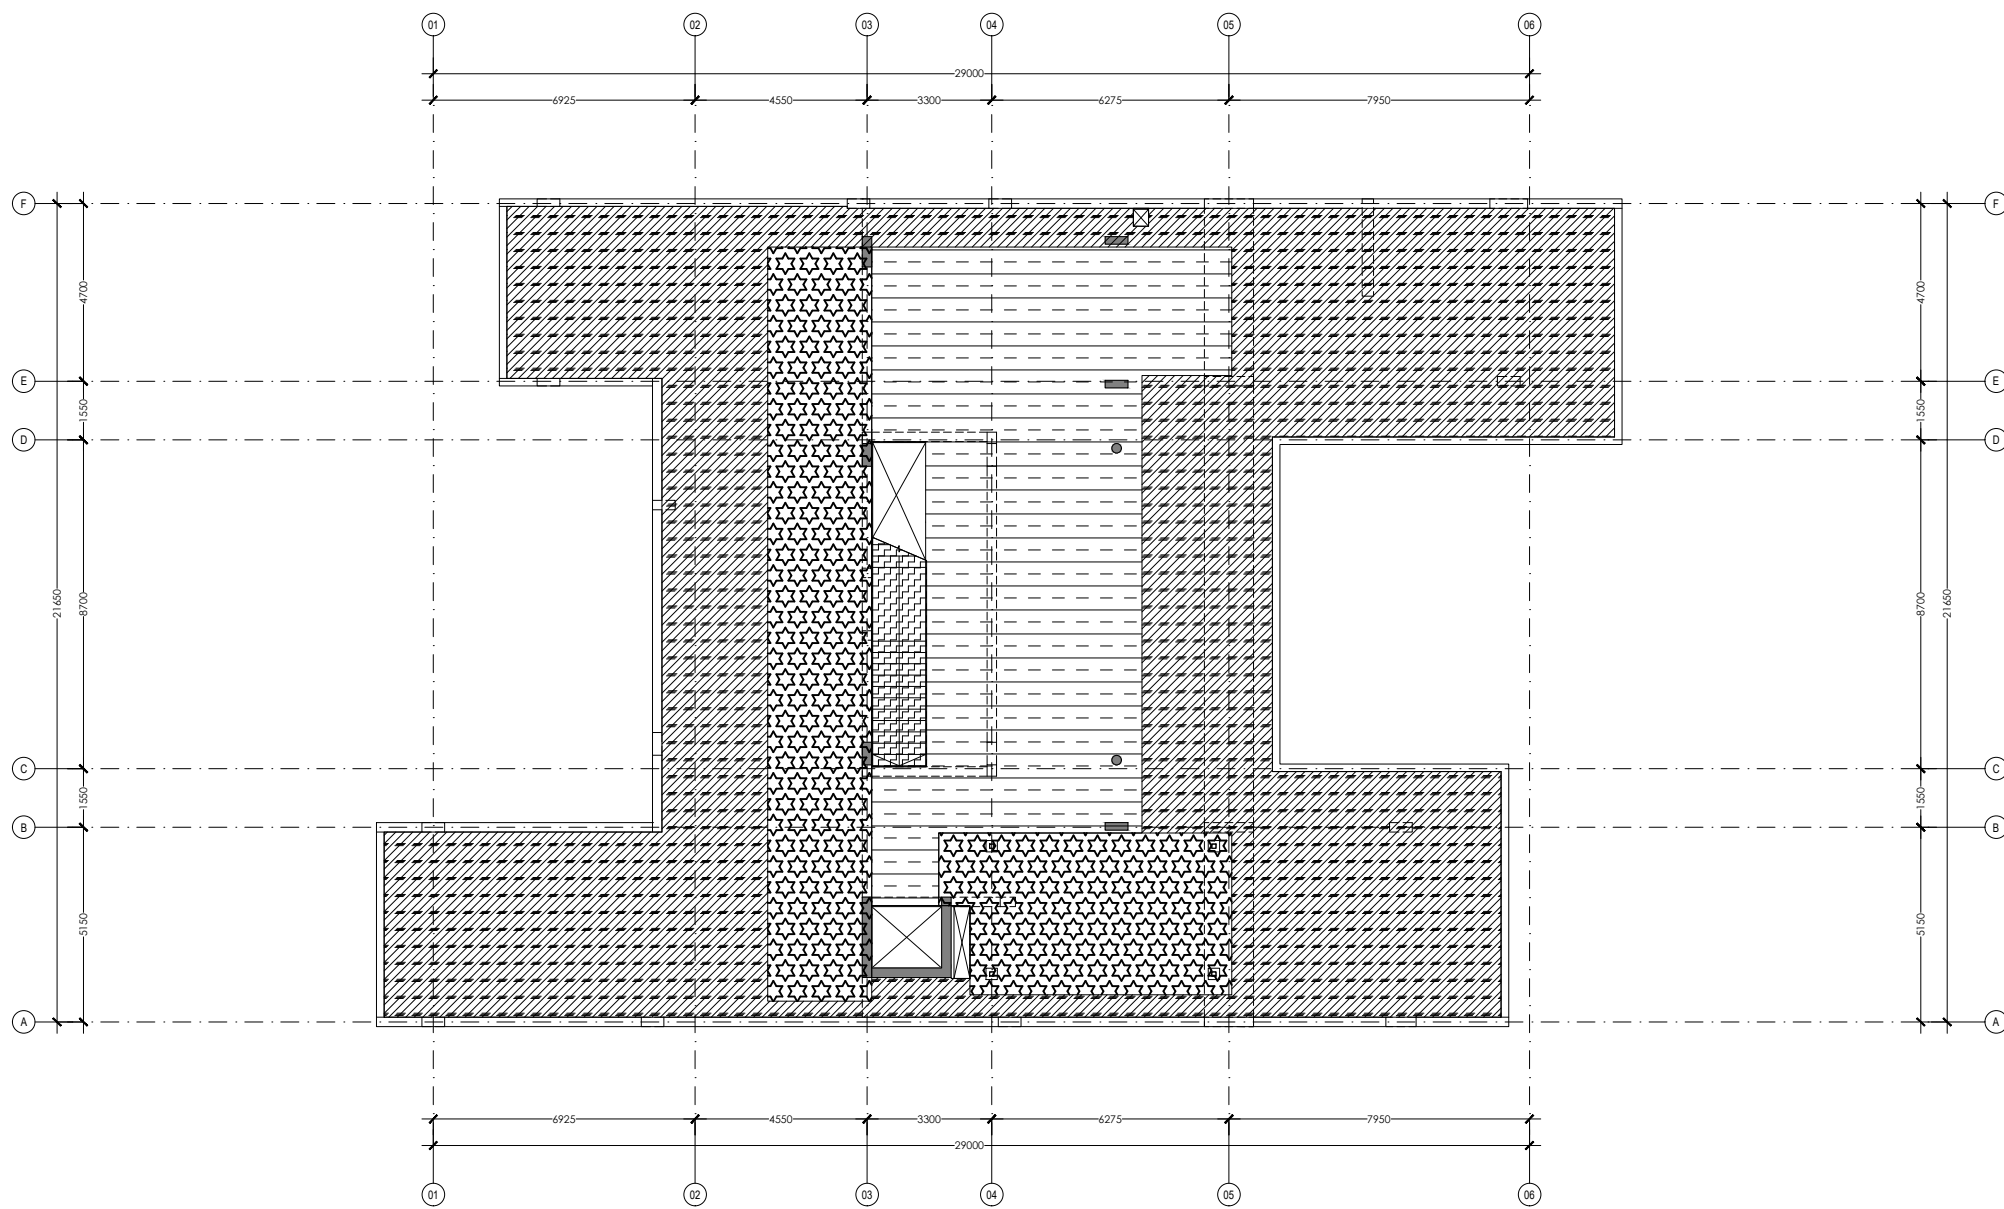


ROOF FLOOR LOADING PLAN
SCALE: 1:250

LOADING PLAN SCHEDULE							
Sr. No.	LEGEND	USAGE	S.I.D.L (KN/m ²)				L.L (Kn/m ²)
			PARTITIONS (KN/m ²)	FINISH (KN/m ²)	CEILING (KN/m ²)	TOTAL (KN/m ²)	
1		PUMP ROOM	3.00	1.50	---	4.50	5.00
2		WATER TANK	---	1.00	---	1.00	20.00
3		RESIDENTIAL	3.00	2.00	---	5.00	2.00
4		PARKING	---	5.00	---	5.00	2.00
5		STAIRS	---	2.50	---	2.50	4.80
6		PLANTER	---	---	---	---	7.00
7		MEP	---	3.00	0.50	3.50	3.50
8		ROOF	---	3.00	0.50	3.50	1.00

LOADING PLAN SCHEDULE
SCALE: NTS

- GENERAL NOTES
- This Drawing Issue has been checked and approved in accordance with the LOCI Quality Management System.
 - All works shall be carried out in accordance with particular & general specifications, in conjunction with relevant conditions of contract.
 - This drawing shall not be used directly for Construction, but for preparation of Shop Drawings in coordination with other disciplines and Suppliers prior to manufacture, delivery and execution on site.
 - All dimensions and levels are in millimeter, unless noted otherwise, only written dimensions to be followed and not scaled from the drawing.
 - All dimensions to be verified at site and coordinated with other disciplines/ manufacturers in the preparation of shop drawings. Any changes shall be validated by the consultant.
 - For elements with indicative design, the contractor / supplier shall submit complete construction details and technical specifications for approval prior to execution. Shop drawings to particularly incorporate details at structural expansion joints as well as expansion / construction joints needed for the respective materials/ finishes / related works.
 - Safety standards and statutory regulations shall be adhered to in the manufacture, supply, storage and installation of all works.
 - Any discrepancy or ambiguity whatsoever with dimensions / details / legends / specifications / etc, shall be brought to the attention of the Consultant and clarification obtained prior to finalization of tender / construction.

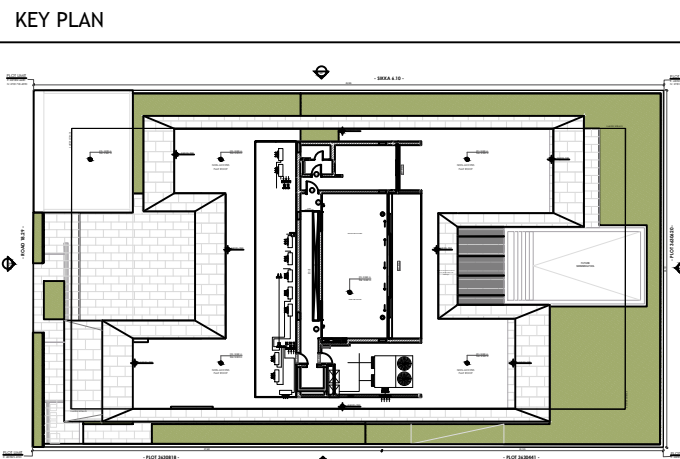

DRAWING REVISIONS				
REV	DATE	DESCRIPTION	CHECKED	APPROVED
00	14.03.2025	ISSUED FOR APPROVAL	AN	BR

CLIENT
TARUN HARISH CHANDRA KHANNA

DRAWING DETAILS
LOADING PLANS

SHEET #
269-S-105

REVISION
R0

ISSUE DATE:
14-03-2025

SCALE @ A1
AS SHOWN

PROJECT DETAILS
KHANNA VILLA



PROJECT LOCATION
PLOT NO. 3630160
Al Manara,
Dubai

PROJECT NUMBER
269

PROJECT PHASE
DETAIL DESIGN

CONSULTANT

LOCI
لوکار

Office M31, KIA Flagship
Building
Sheikh Zayed Rd, Al Quoz 1
P. O. Box 72928, Dubai
T +971 4 357 6573
W www.loci.ae