


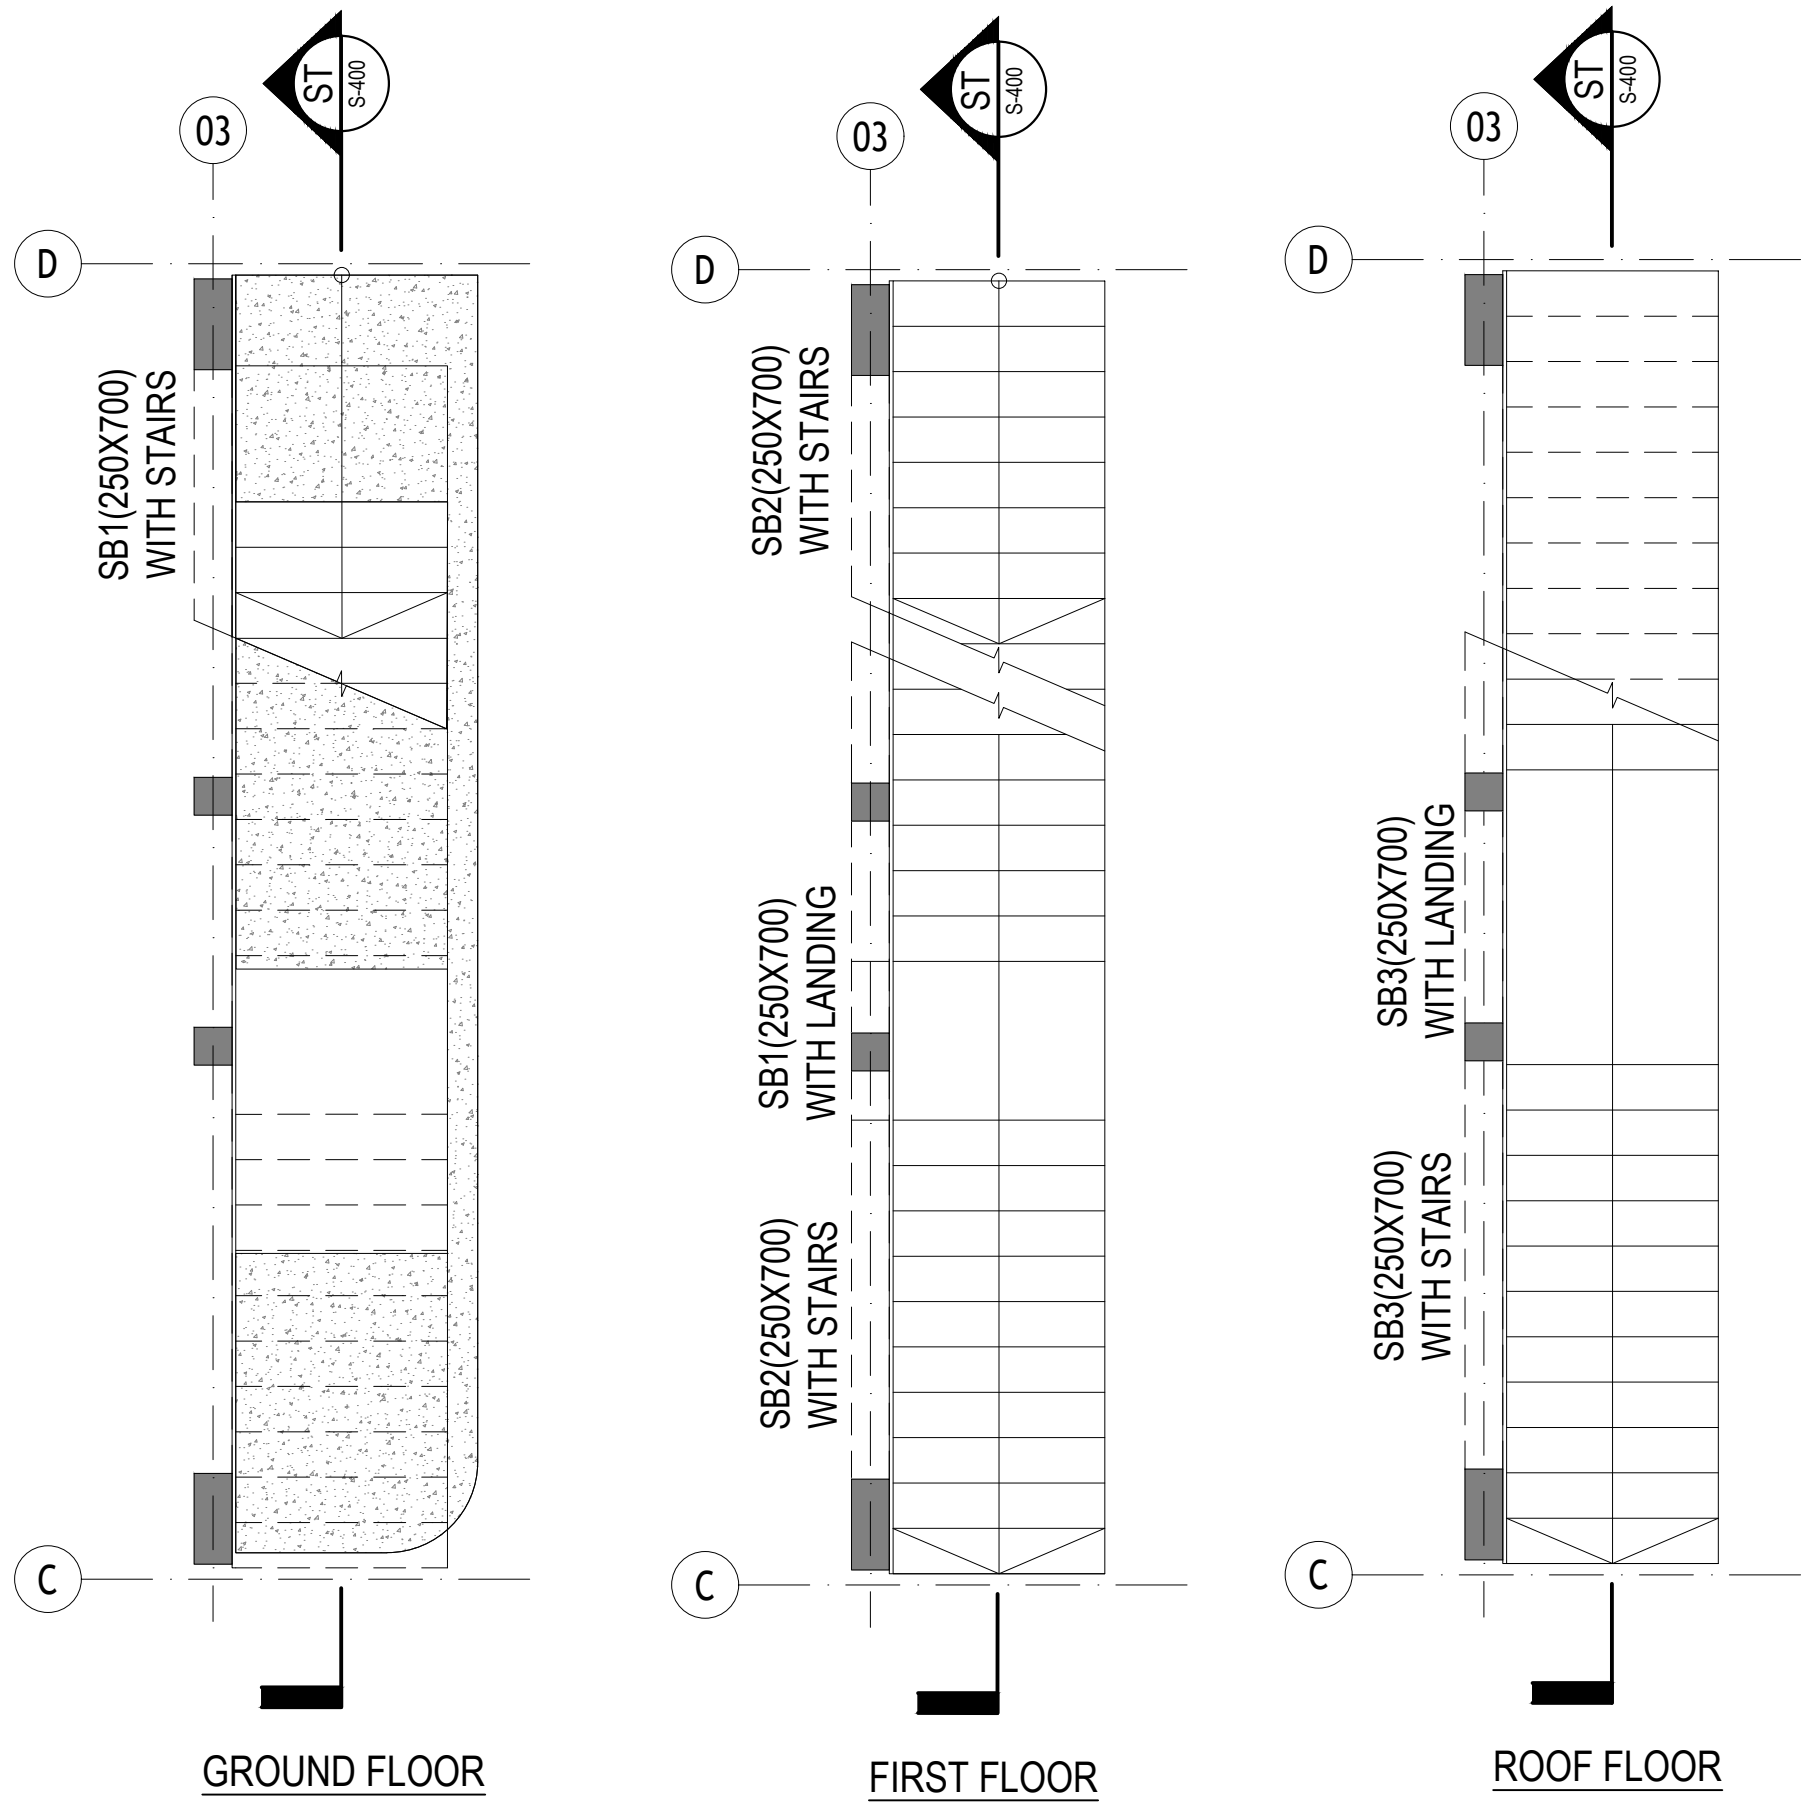


STAIRCASE- FLOOR PLANS

SCALE: 1:50

- NOTES FOR STAIRS:**
- * ALL STAIR STEEL ELEMENTS AND WOODEN STEPS TO BE DESIGNED BY THE CONTRACTOR.
 - * STEEL TO STEEL AND STEEL TO CONCRETE CONNECTIONS SHALL BE DESIGNED AND DETAILED BY THE CONTRACTOR
 - * BASED ON THE DESIGN FORCES FOUND IN THE CONTRACTOR DETAILED DESIGN
 - * CONTRACTOR HAVE TO PROVIDE THE FINAL REACTIONS FROM THE DETAILED DESIGN MODELS OF STEEL STRUCTURE
 - * TO VERIFY THE DESIGN OF THE SUPPORTING CONCRETE BEAMS / COLUMNS.
 - * LIVE LOADS CONSIDERED ON STAIRS TO BE 4.80 kN/m², AND THE SUPER IMPOSED DEAD LOAD TO BE CALCULATED APPROXIMATELY ACCORDING TO THE SELF WEIGHT OF ALL STEEL ELEMENTS, WOODEN STEPS AND FINISHES .

STAIRCASE NOTES

SCALE: N.T.S.

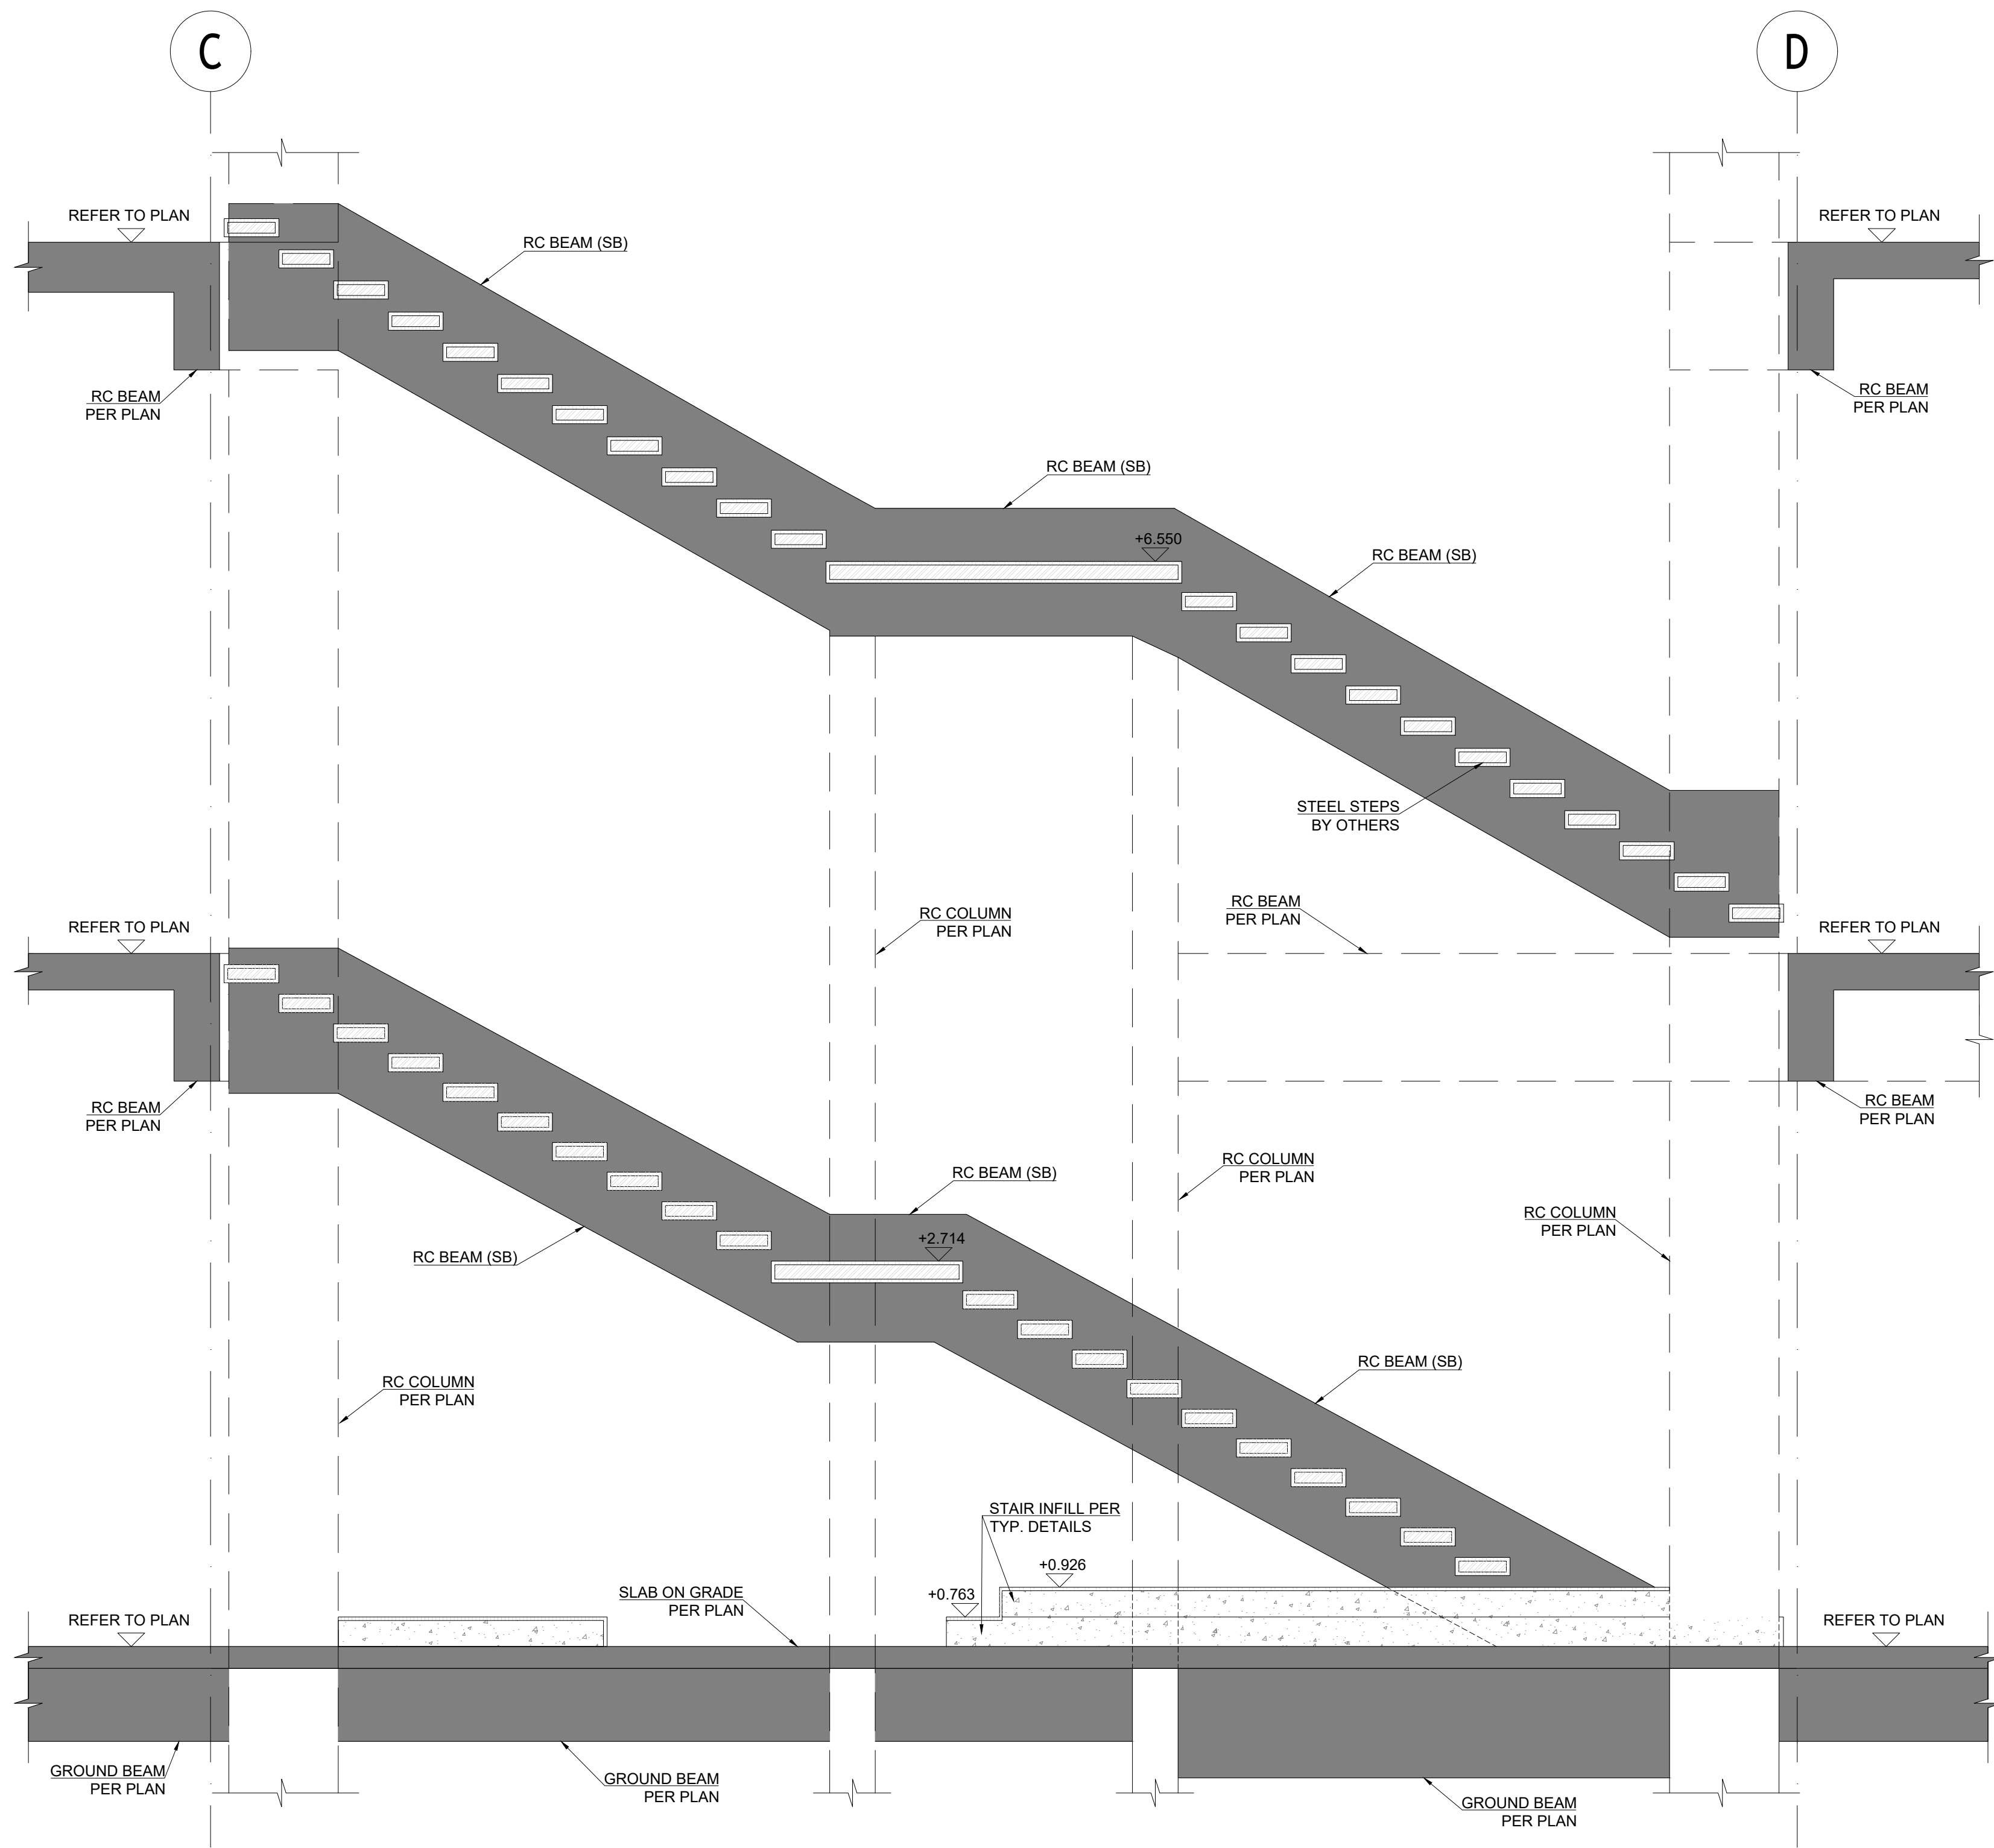

STAIRCASE SECTION

SCALE: 1:50

BEAM REINFORCEMENT SCHEDULE FOR STAIRS


BEAM (MARK)	BOTTOM REINFORCEMENT	TOP REINFORCEMENT	LINKS	SIDE BARS EACH FACE	LINK ARRANGEMENT	REMARKS
SB1	3T20	2T16+2T16	2L-T12-150	2T12		
SB2	2T20	3T16	2L-T10-150	2T12		
SB3	3T16	2T16	2L-T10-150	2T12		

STAIRCASE BEAMS SCHEDULE

SCALE: NTS

- GENERAL NOTES**
1. This Drawing Issue has been checked and approved in accordance with the LOCI Quality Management System.
 2. All works shall be carried out in accordance with particular & general specifications, in conjunction with relevant conditions of contract.
 3. This drawing shall not be used directly for Construction, but for preparation of Shop Drawings in coordination with other disciplines and Suppliers prior to manufacture, delivery and execution on site.
 4. All dimensions and levels are in millimeter, unless noted otherwise, only written dimensions to be followed and not scaled from the drawing.
 5. All dimensions to be verified at site and coordinated with other disciplines/ manufacturers in the preparation of shop drawings. Any changes shall be validated by the consultant.
 6. For elements with indicative design, the contractor / supplier shall submit complete construction details and technical specifications for approval prior to execution, shop drawings to particularly incorporate details at structural expansion joints as well as expansion / construction joints needed for the respective materials/ finishes / related works.
 7. Safety standards and statutory regulations shall be adhered to in the manufacture, supply, storage and installation of all works.
 8. Any discrepancy or ambiguity whatsoever with dimensions / details / legends / specifications / etc, shall be brought to the attention of the Consultant and clarification obtained prior to finalization of tender / construction.

KEY PLAN

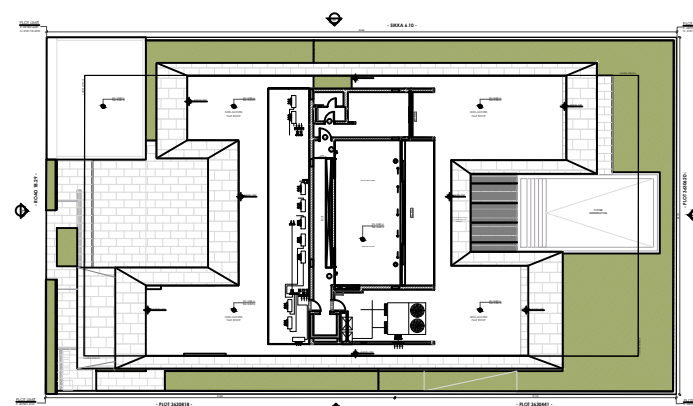

DRAWING REVISIONS

REV	DATE	DESCRIPTION	CHECKED	APPROVED
00	14.03.2025	ISSUED FOR APPROVAL	AN	BR

CLIENT

TARUN HARISH CHANDRA KHANNA

DRAWING DETAILS

STAIR CASE DETAILS

SHEET #

269-S-400

REVISION

R0

ISSUE DATE:

14-03-2025

SCALE @ A1

AS SHOWN

PROJECT DETAILS

KHANNA VILLA



PROJECT LOCATION

PLOT NO. 3630160
Al Manara,
Dubai

PROJECT NUMBER

269

PROJECT PHASE

DETAIL DESIGN

CONSULTANT

LOCI
لوکار

Office M31, KIA Flagship
Building
Sheikh Zayed Rd, Al Quoz 1
P. O. Box 72928, Dubai
T +971 4 357 6573
W www.loci.ae