



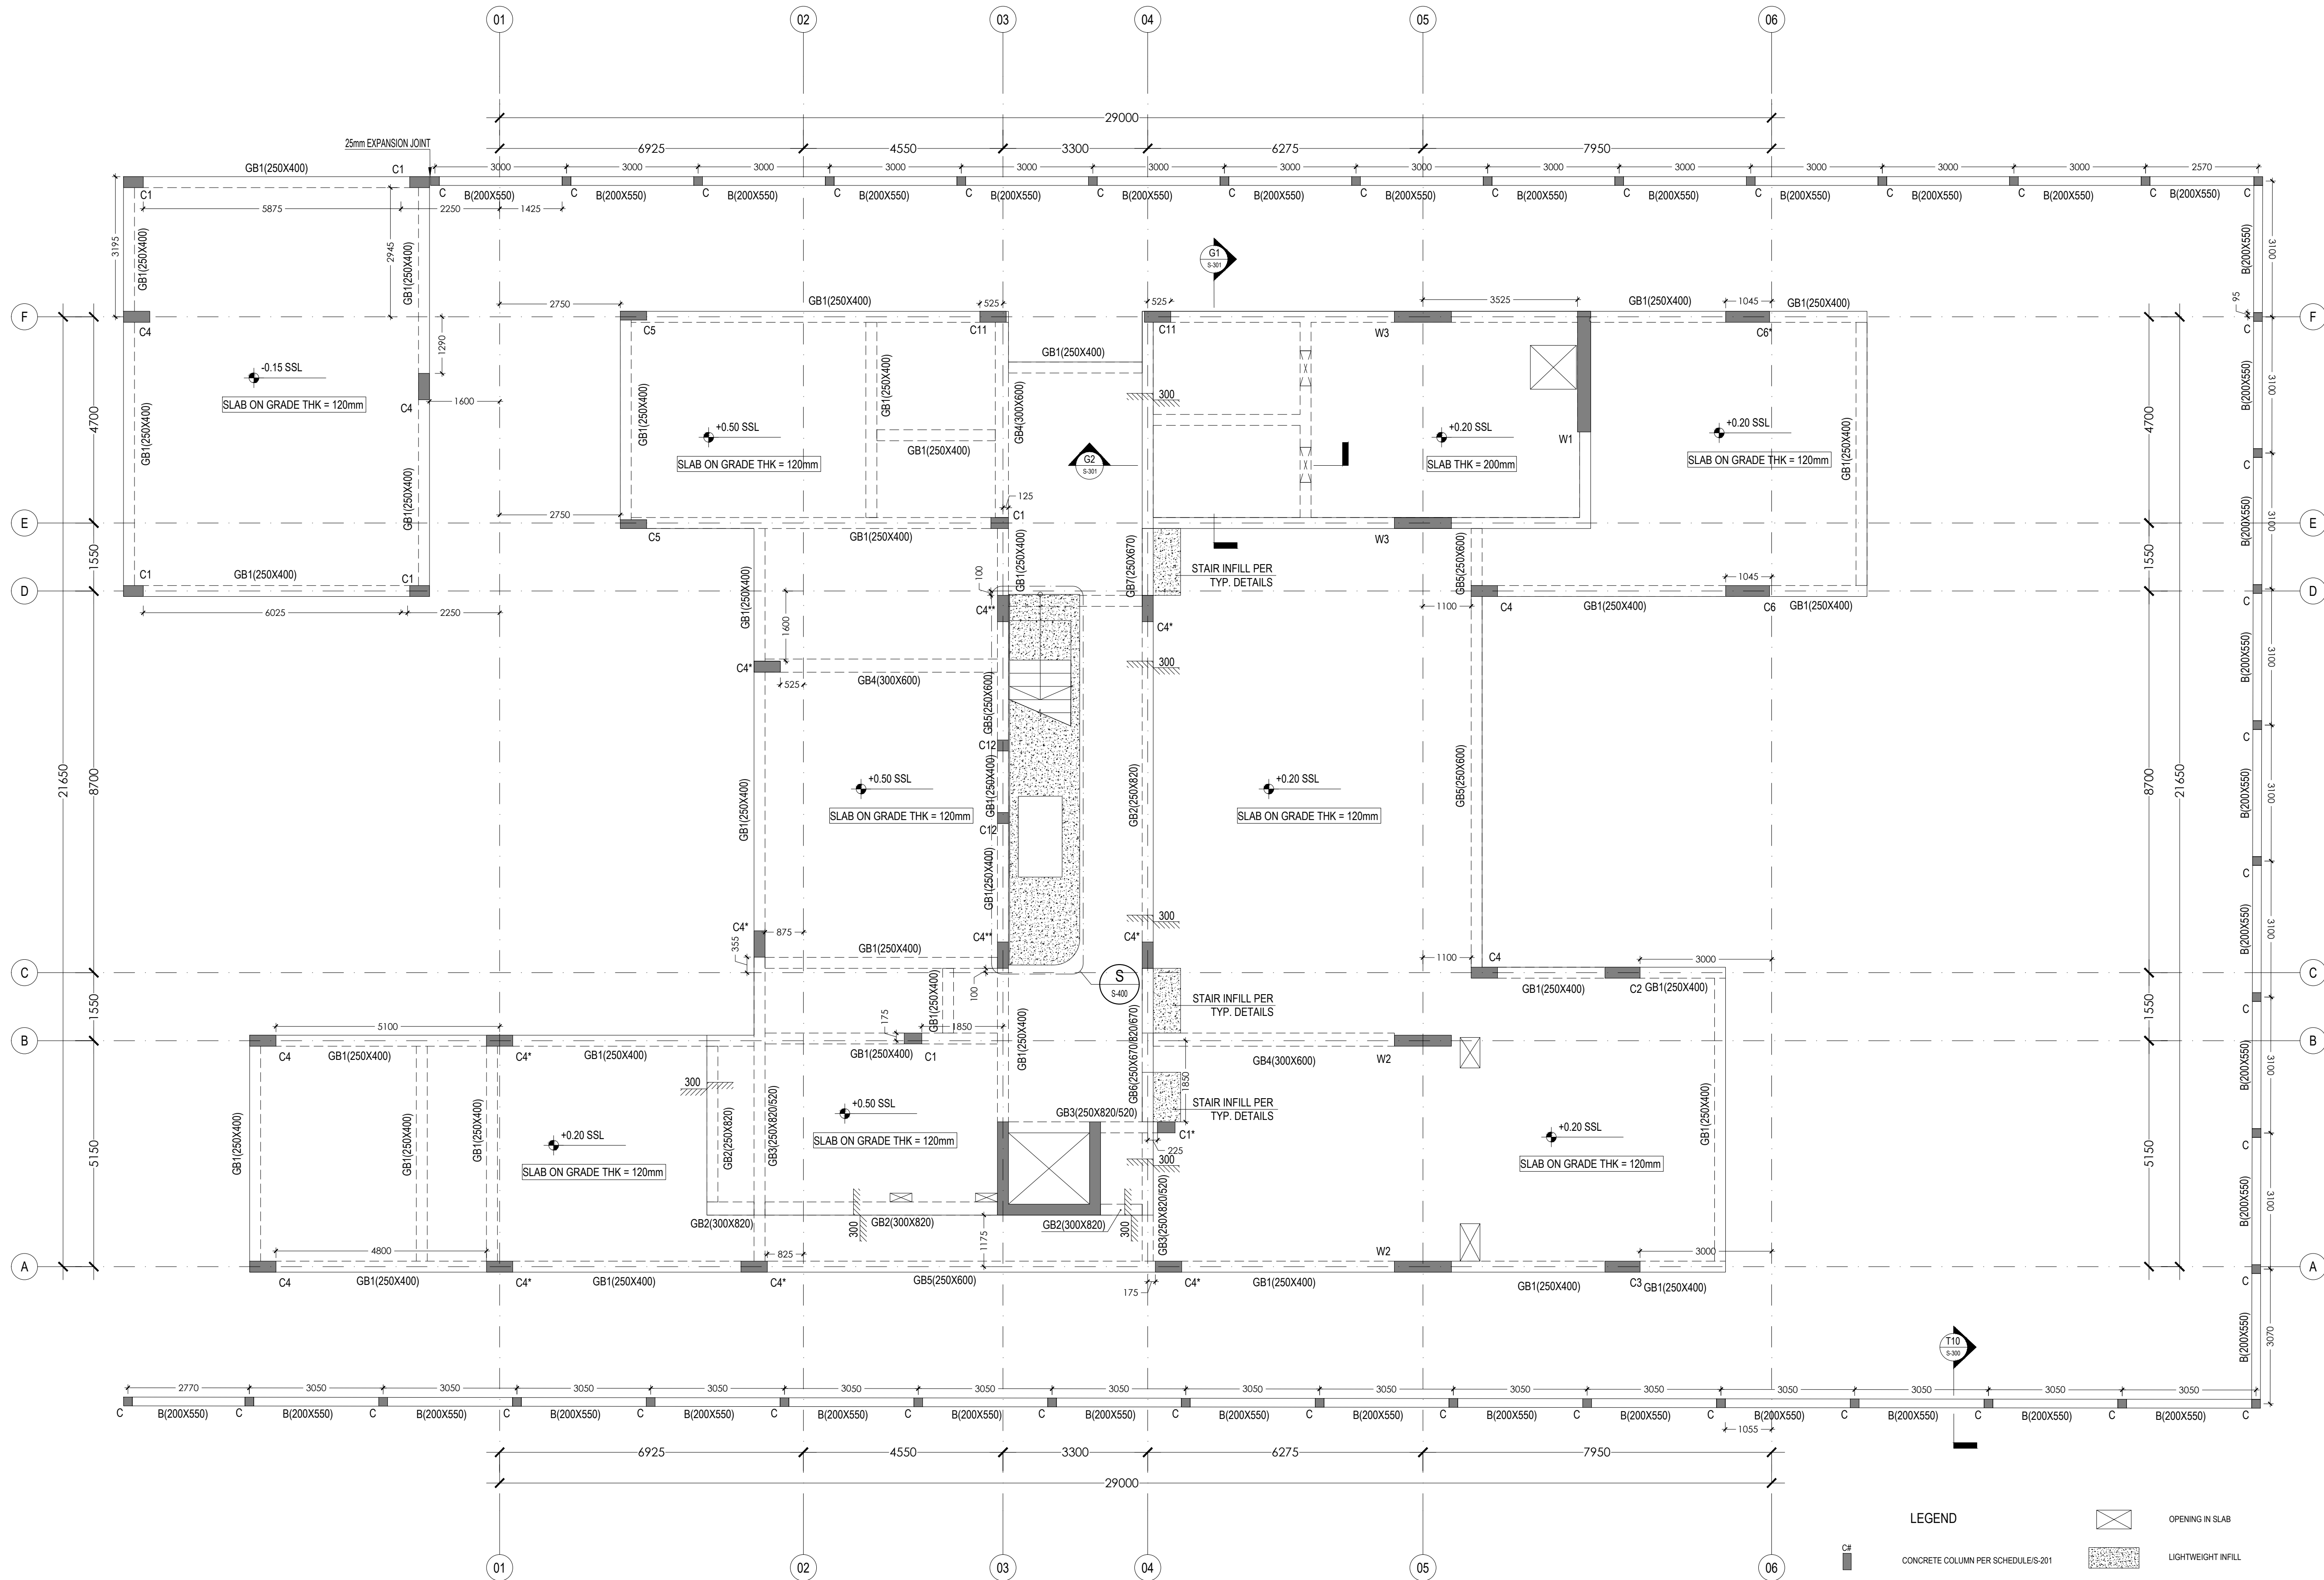

1 GROUND FLOOR GENERAL ARRANGEMENT PLAN
SCALE: 1:75

- GENERAL NOTES
1. This Drawing Issue has been checked and approved in accordance with the LOCI Quality Management System.
 2. All works shall be carried out in accordance with particular B general specifications, in conjunction with relevant conditions of contract.
 3. This drawing shall not be used directly for Construction, but for preparation of Shop Drawings in coordination with other disciplines and Suppliers prior to manufacture, delivery and execution on site.
 4. All dimensions and levels are in millimeter, unless noted otherwise, only written dimensions to be followed and not scaled from the drawing.
 5. All dimensions to be verified at site and coordinated with other disciplines/ manufacturers in the preparation of shop drawings. Any changes shall be validated by the consultant.
 6. For elements with indicative design, the contractor / supplier shall submit complete construction details and technical specifications for approval prior to execution, shop drawings to particularly incorporate details at structural expansion joints as well as expansion / construction joints needed for the respective materials/ finishes / related works.
 7. Safety standards and statutory regulations shall be adhered to in the manufacture, supply, storage and installation of all works.
 8. Any discrepancy or ambiguity whatsoever with dimensions / details / legends / specifications / etc, shall be brought to the attention of the Consultant and clarification obtained prior to finalization of tender / construction.

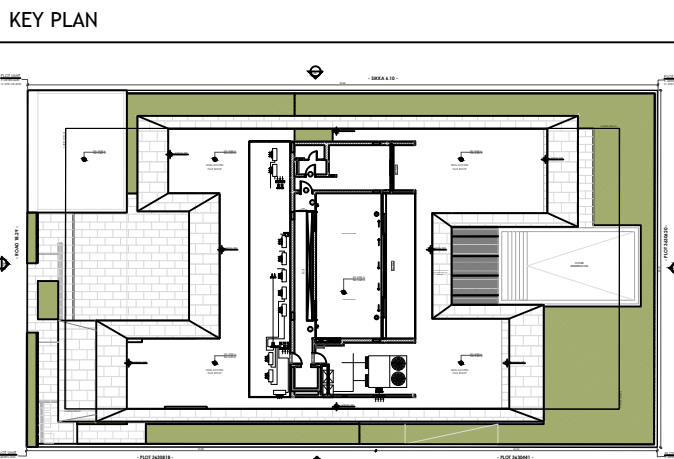

DRAWING REVISIONS				
REV	DATE	DESCRIPTION	CHECKED	APPROVED
00	14.03.2025	ISSUED FOR APPROVAL	AN	BR

CLIENT
TARUN HARISH CHANDRA KHANNA

DRAWING DETAILS
GROUND FLOOR
GENERAL ARRANGEMENT PLAN
SHEET #
269-S-101-A
REVISION
R0
ISSUE DATE:
14-03-2025
SCALE @ A1
AS SHOWN



PROJECT LOCATION
PLOT NO. 3630160
Al Manara,
Dubai
PROJECT NUMBER
269

PROJECT PHASE
DETAIL DESIGN

CONSULTANT
LOCI
لوکار
Office M31, KIA Flagship
Building
Sheikh Zayed Rd, Al Quoz 1
P. O. Box 72928, Dubai
T +971 4 357 6573
W www.loci.ae

- LEGEND
- CONCRETE COLUMN PER SCHEDULE/S-201
 - CONCRETE WALL PER SCHEDULE/S-202
 - CONCRETE COLUMN/WALL BELOW
 - CONCRETE BEAM PER SCHEDULE/S-200
 - OPENING IN SLAB
 - LIGHTWEIGHT INFILL
 - CHANGE IN SLAB LEVEL
 - STRUCTURAL SLAB LEVEL
 - TOP OF BEAM/UPSTAND LEVEL