



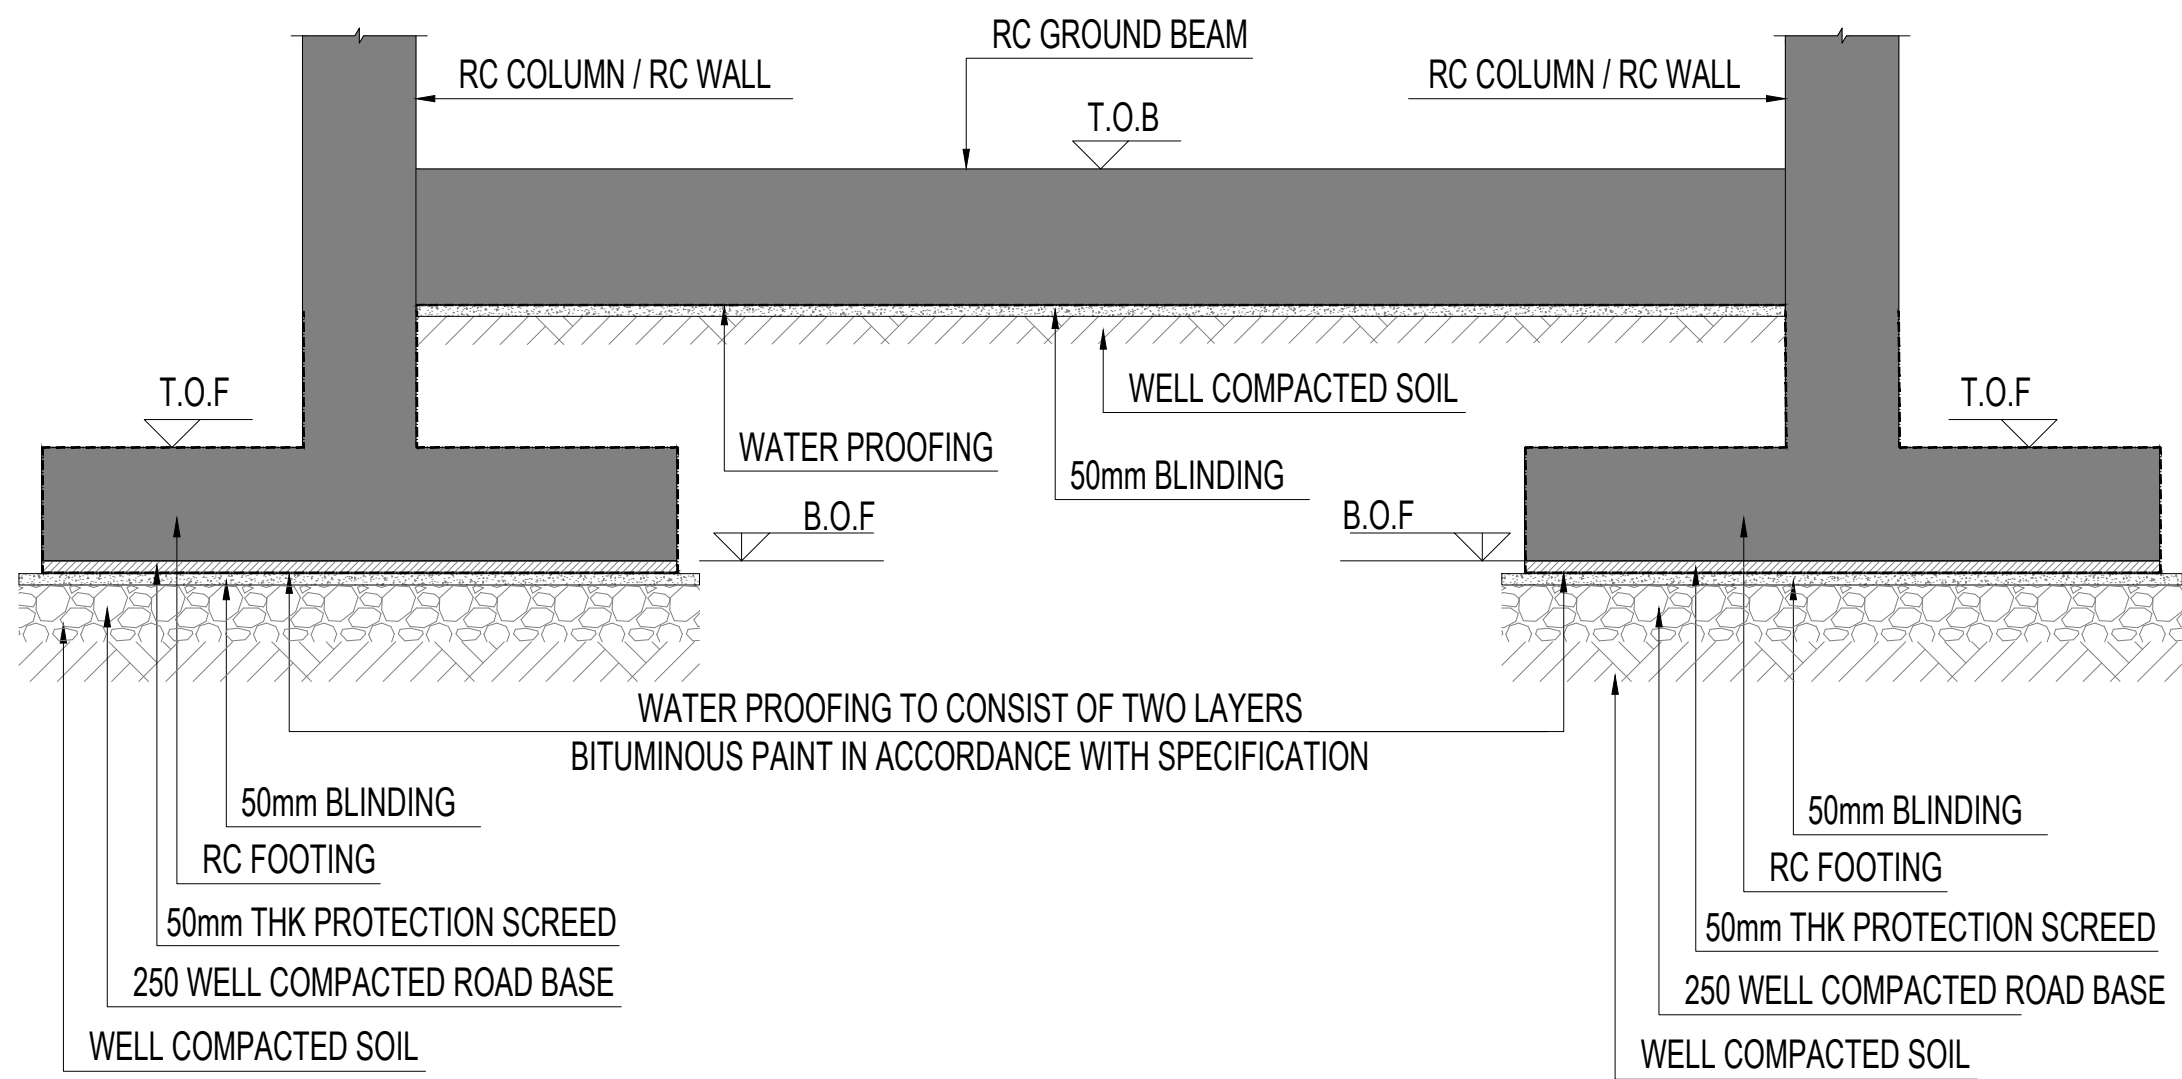


GROUND BEAM TYP. SECTION

SCALE: 1:25

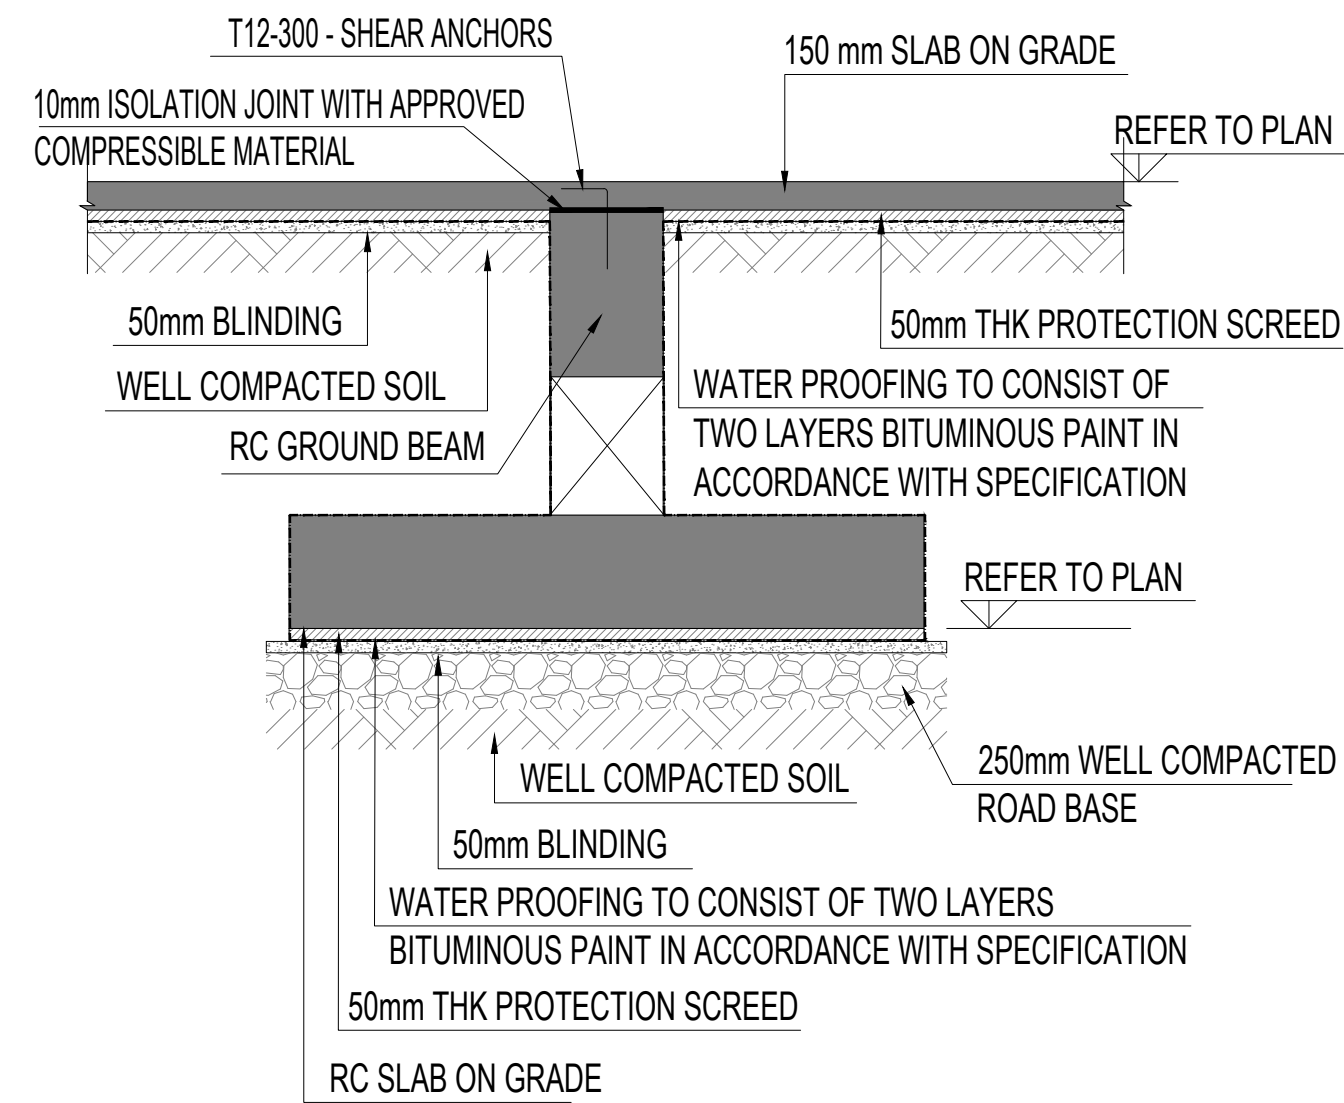


TYP. CONNECTION BETWEEN SLAB ON GRADE AND RC COLUMN/WALL

SCALE: 1:25

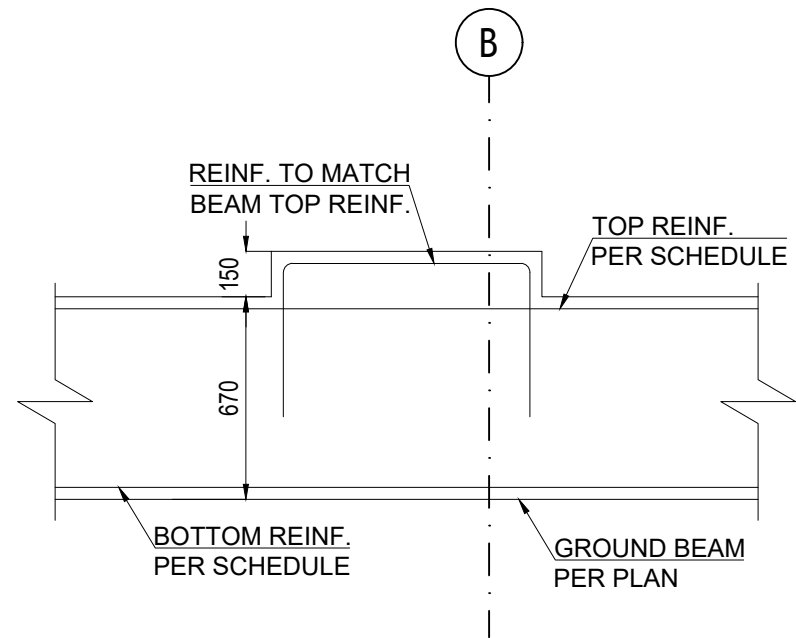


GROUND BEAM BETWEEN STAIRS INFILL

SCALE: 1:25

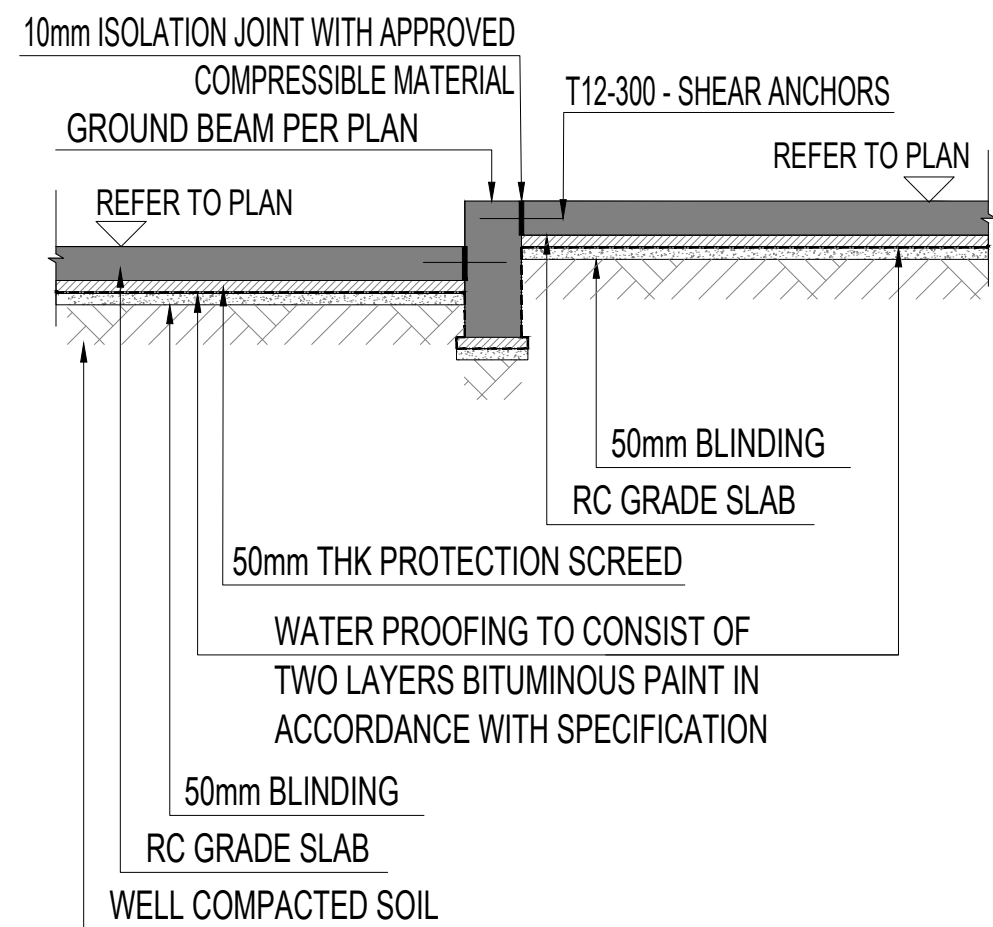


TYP. CONNECTION OF STEPPED SOG TO GB

SCALE: 1:25

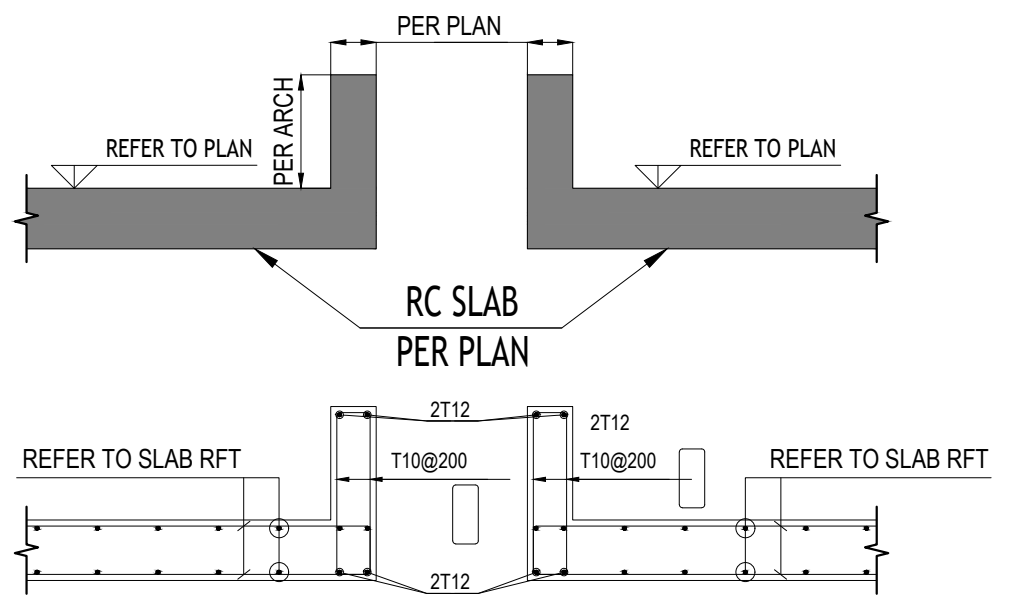


TYP. UPSTAND SECTION

SCALE: 1:25

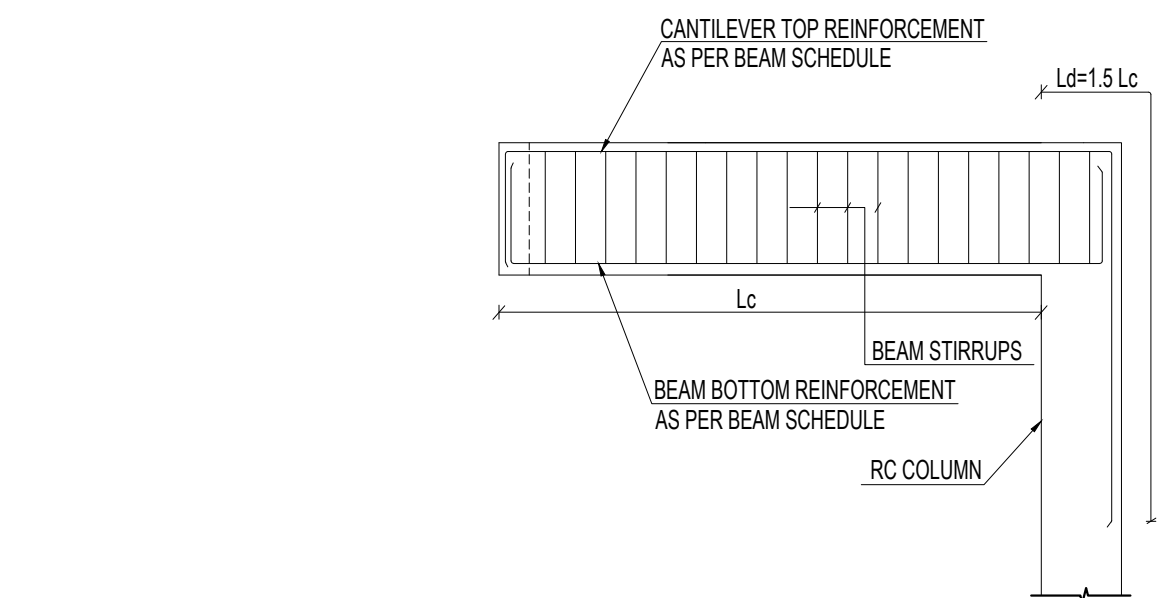


TYP. REINF. DETAIL OF CANTILEVER BEAMS WITH BACKSPAN

SCALE: 1:25

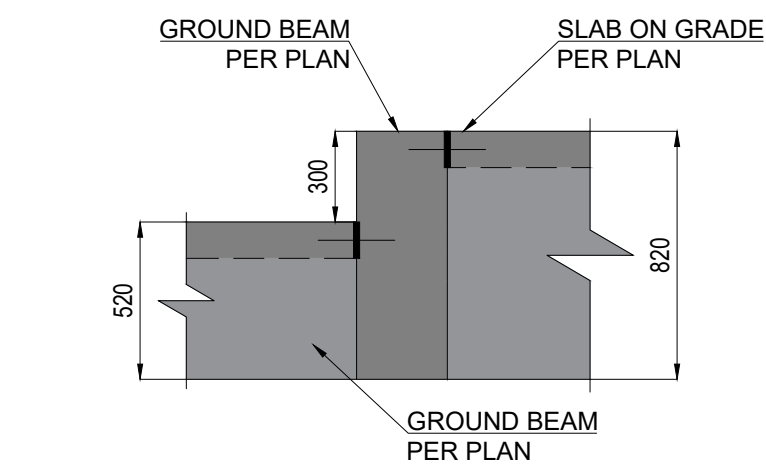


TYP. CONNECTION BETWEEN STEPPED SOG AND GB

SCALE: 1:25

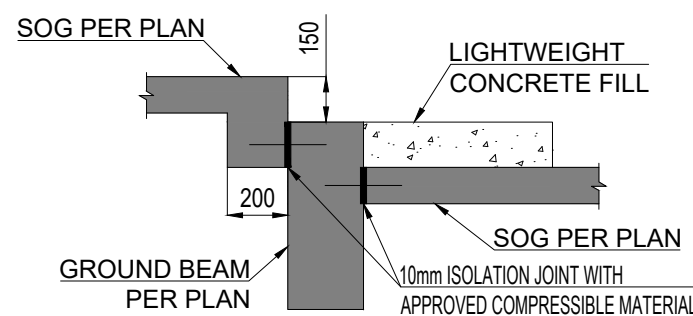


TYP. CONNECTION AT INFILL STAIRS

SCALE: 1:25

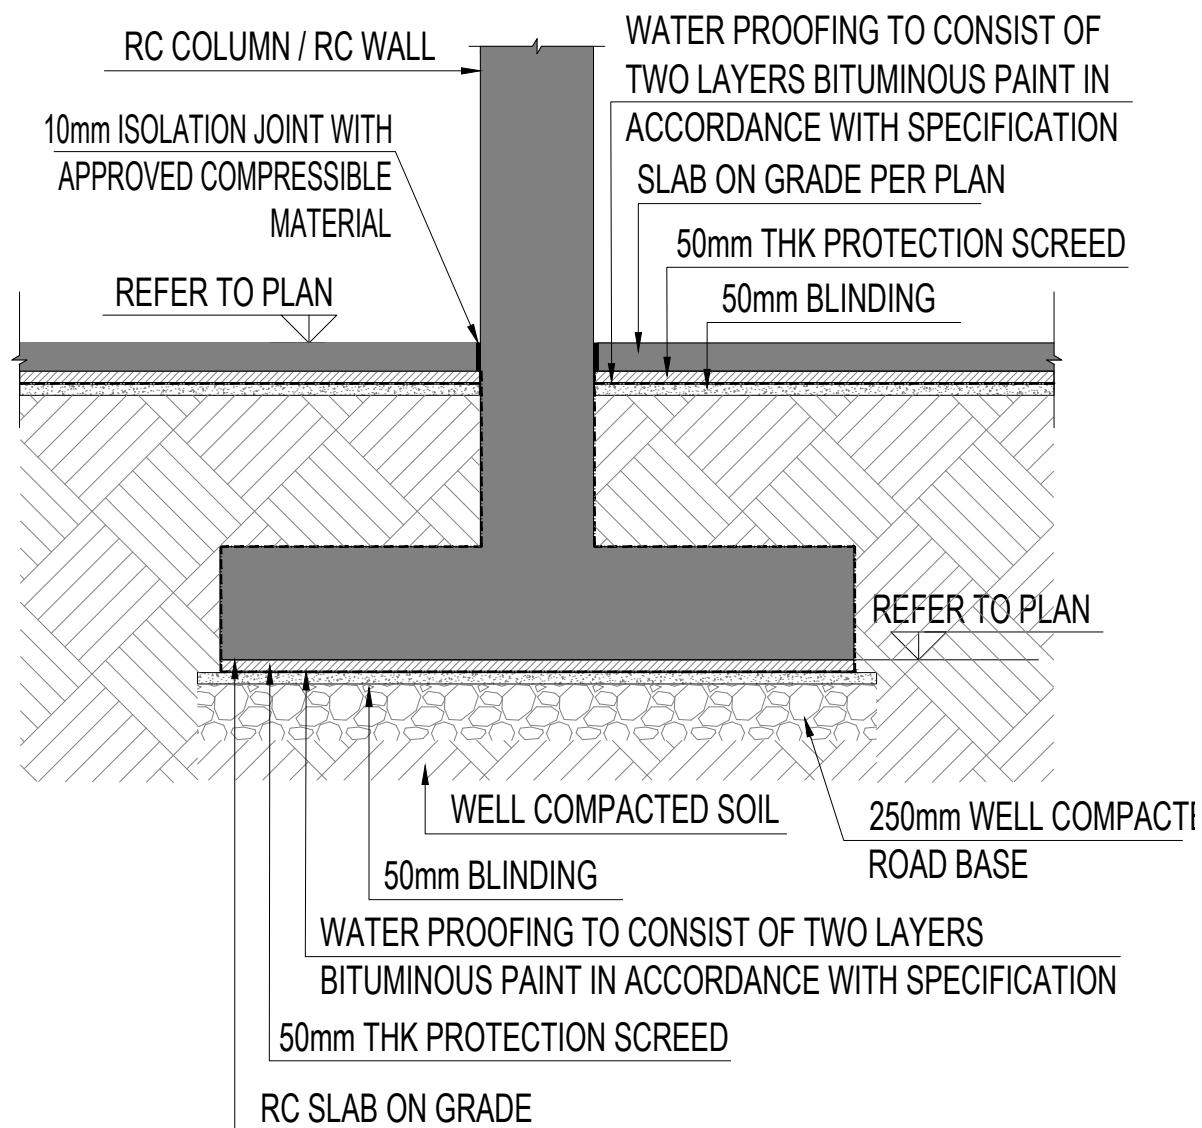

TYP. CONNECTION BETWEEN SOG AND RC COLUMN/WALL


SCALE: 1:25

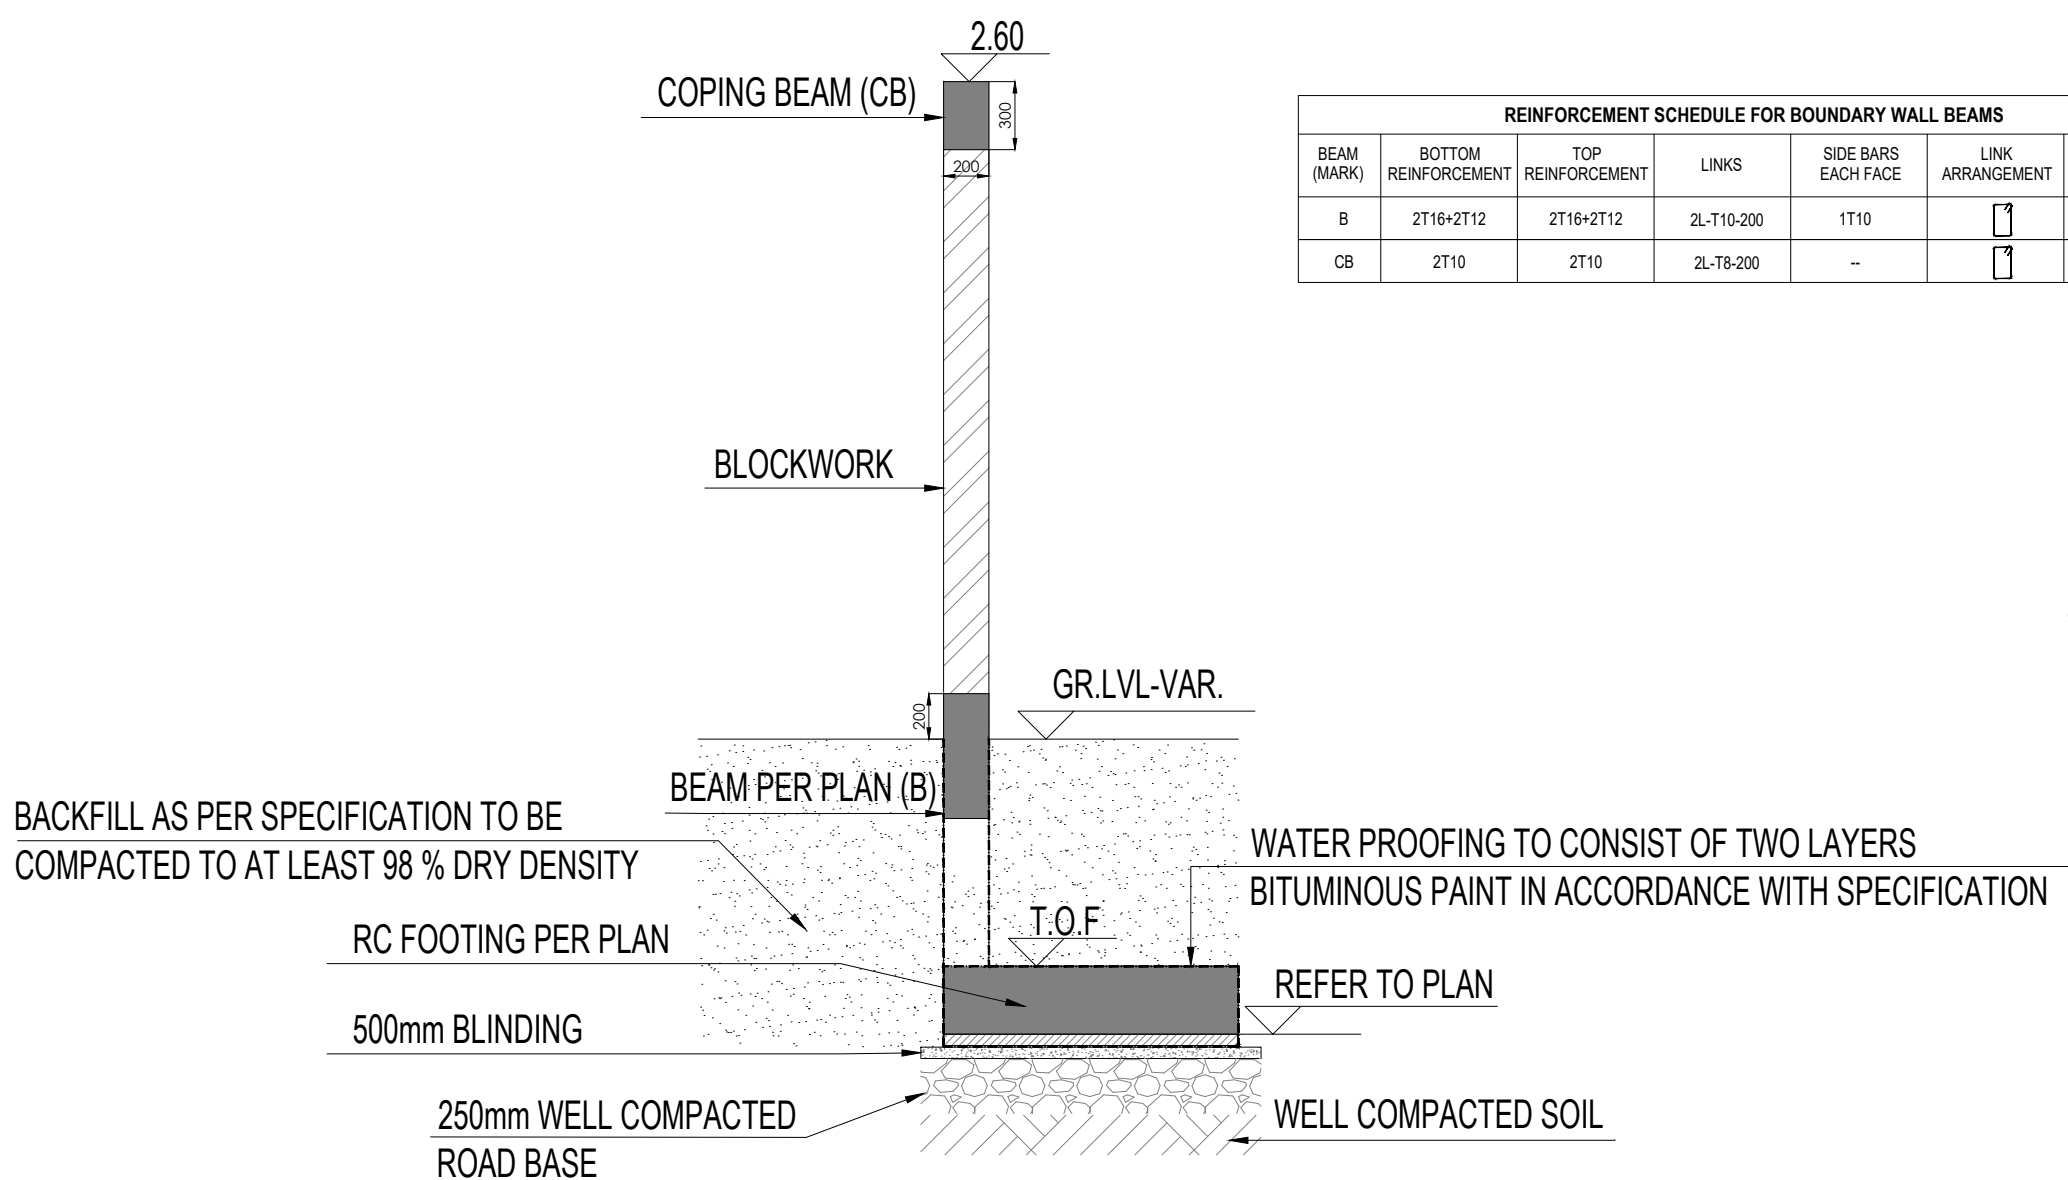

BOUNDARY WALL TYPICAL DETAILS

SCALE: 1:25


REINFORCEMENT SCHEDULE FOR BOUNDARY WALL BEAMS						
BEAM (MARK)	BOTTOM REINFORCEMENT	TOP REINFORCEMENT	LINKS	SIDE BARS EACH FACE	LINK ARRANGEMENT	REMARKS
B	2T16+2T12	2T16+2T12	2L-T10-200	1T10		
CB	2T10	2T10	2L-T8-200	--		

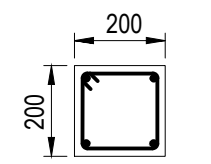

REINF. : 4T16
STIRRUP : T10-200

COLUMN "C"

- GENERAL NOTES**
- This Drawing Issue has been checked and approved in accordance with the LOCI Quality Management System.
 - All works shall be carried out in accordance with particular & general specifications, in conjunction with relevant conditions of contract.
 - This drawing shall not be used directly for Construction, but for preparation of Shop Drawings in coordination with other disciplines and Suppliers prior to manufacture, delivery and execution on site.
 - All dimensions and levels are in millimeter, unless noted otherwise, only written dimensions to be followed and not scaled from the drawing.
 - All dimensions to be verified at site and coordinated with other disciplines/ manufacturers in the preparation of shop drawings. Any changes shall be validated by the consultant.
 - For elements with indicative design, the contractor / supplier shall submit complete construction details and technical specifications for approval prior to execution, shop drawings to particularly incorporate details at structural expansion joints as well as expansion / construction joints needed for the respective materials/ finishes / related works.
 - Safety standards and statutory regulations shall be adhered to in the manufacture, supply, storage and installation of all works.
 - Any discrepancy or ambiguity whatsoever with dimensions / details / legends / specifications / etc., shall be brought to the attention of the Consultant and clarification obtained prior to finalization of tender / construction.

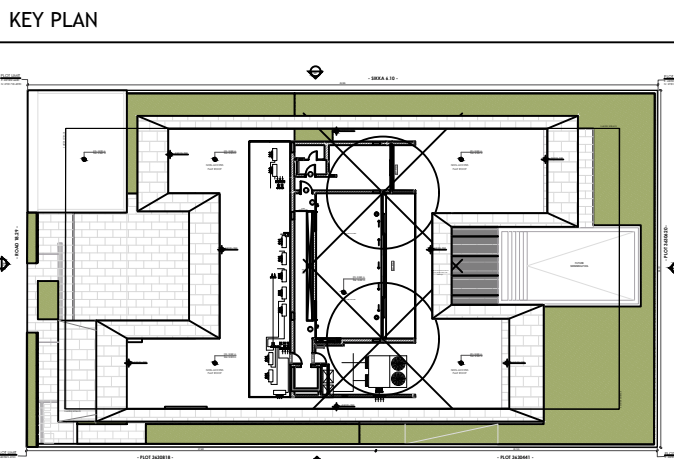

DRAWING REVISIONS				
REV	DATE	DESCRIPTION	CHECKED	APPROVED
00	14.03.2023	ISSUED FOR APPROVAL	AN	BR

CLIENT
TARUN HARISH CHANDRA KHANNA

DRAWING DETAILS
SECTIONS DETAILS - (SHEET 1 OF 2)

SHEET #
269-S-300

REVISION
R0

ISSUE DATE:
14-03-2025

SCALE @ A1
AS SHOWN



PROJECT LOCATION
PLOT NO. 3630160
Al Manara,
Dubai

PROJECT NUMBER
269

PROJECT PHASE
DETAIL DESIGN

CONSULTANT
LOCI
لوکار

Office M31, KIA Flagship Building
Sheikh Zayed Rd, Al Quoz 1
P. O. Box 72928, Dubai
T +971 4 357 6573
W www.loci.ae