



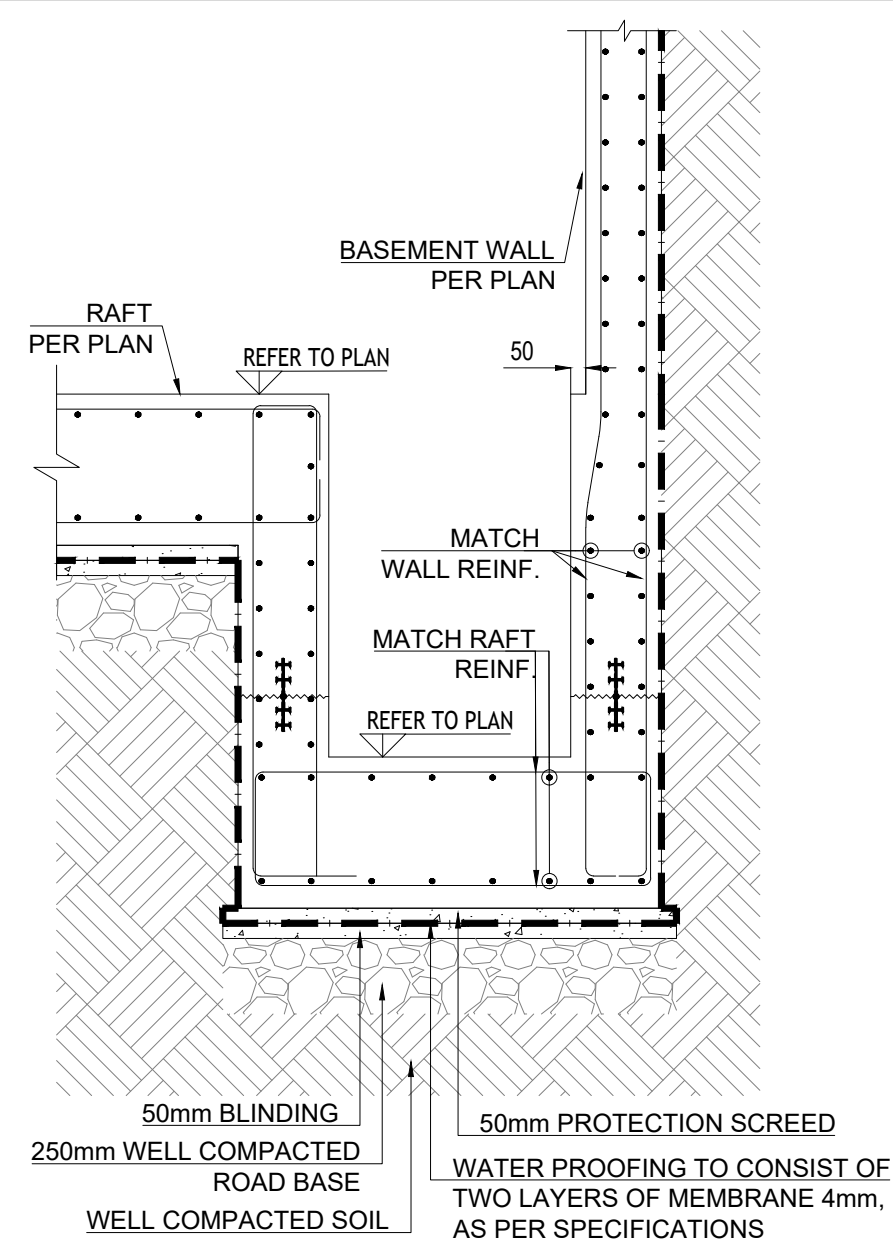


B4
S-100

SUMP PIT SECTION
SCALE: 1:25

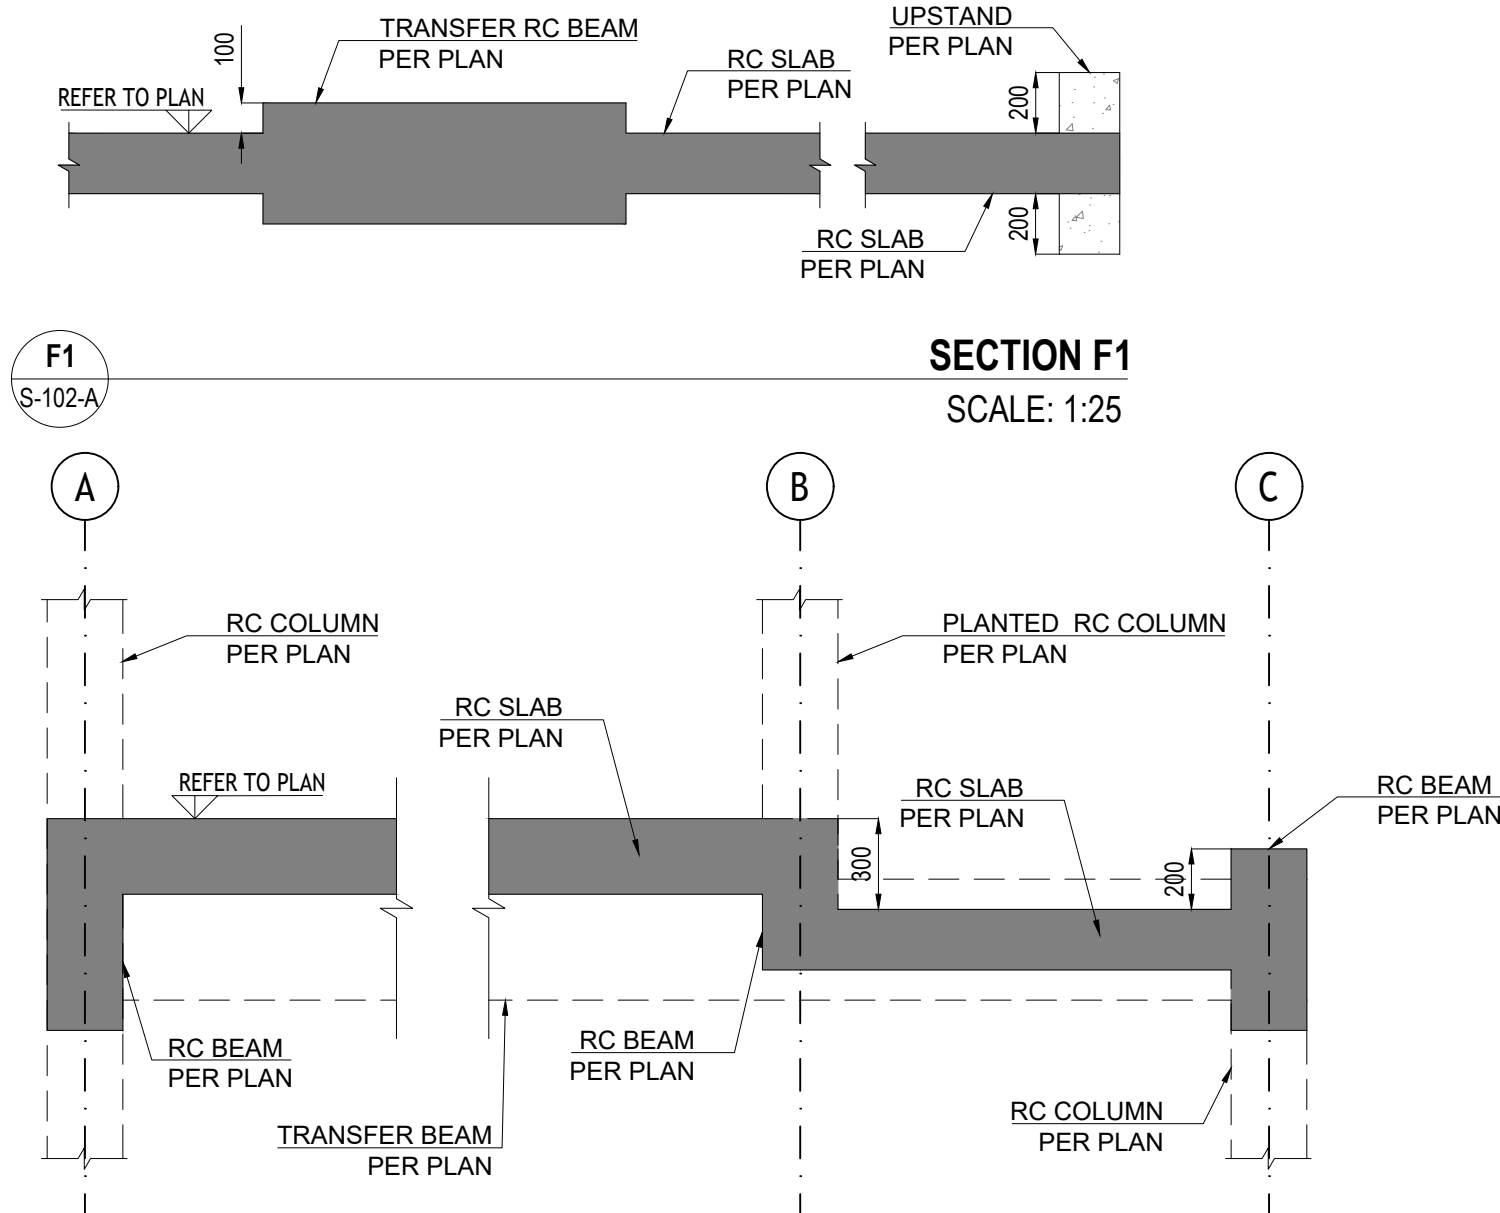

F2
TRANSFER BEAM SECTION
S-102-A
SCALE: 1:25

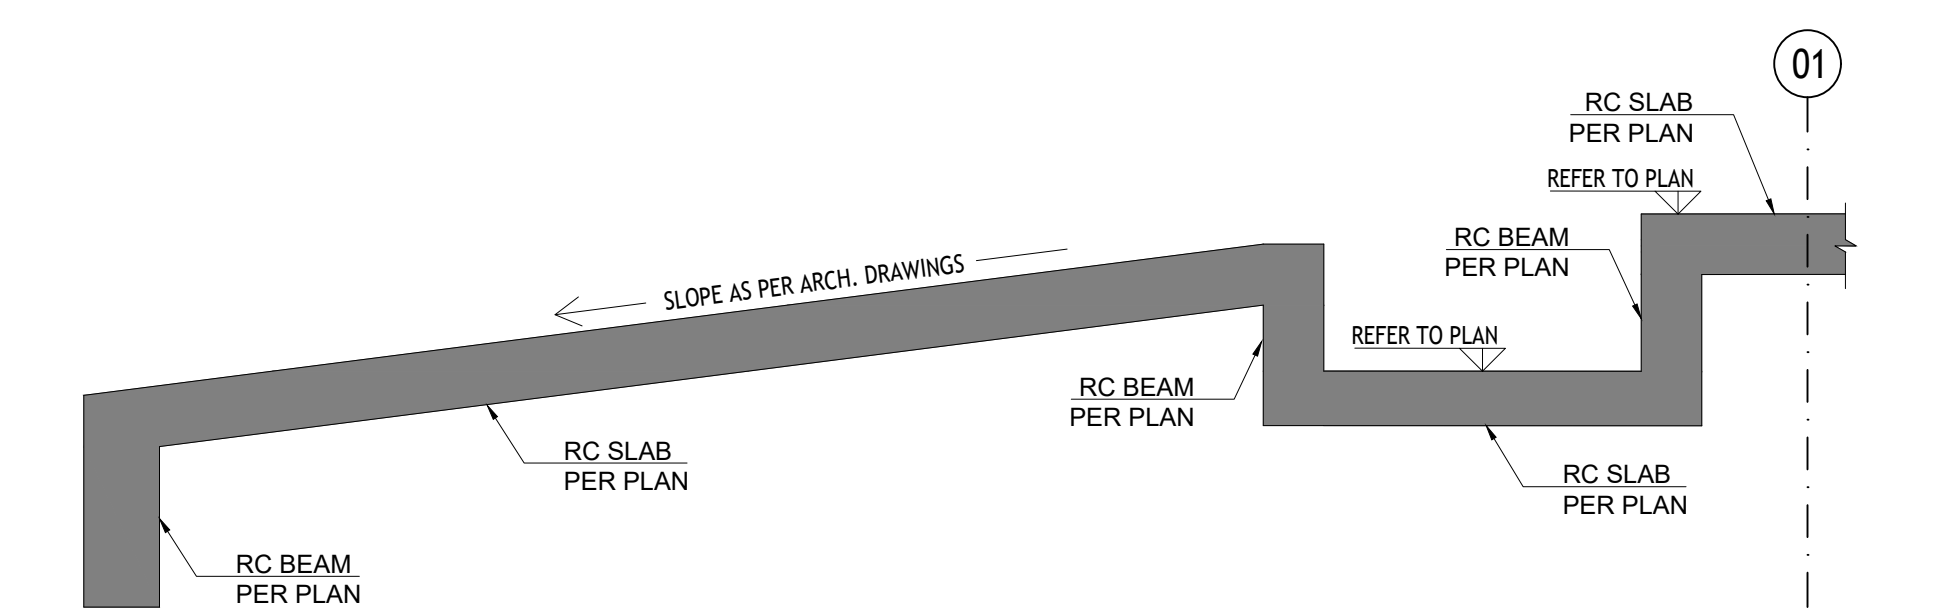

UR1 SECTION UR1
S-104-A SCALE: 1:25



G2 **UNDERGROUND WATER TANK SECTION B**
 S-101-A SCALE: 1:25

03 UPSTAND
REF PLAN



KEY PLAN

Diagram illustrating the key plan of the building, showing the layout of the main floor. The plan includes a large central hall with a circular area, a staircase, and various rooms. The building is surrounded by a green area, and a north arrow is present.

CLIENT

TARUN HARISH CHANDRA KHANNA

DRAWING DETAILS

SECTIONS DETAILS - (SHEET 2 OF 2)

SHEET #
269-S-301

REVISION	ISSUE DATE:	SCALE @ A1
R0	14-03-2025	AS SHOWN

PROJECT DETAILS

KHANNA VILLA



PROJECT LOCATION
PLOT NO. 3630160
Al Manara,
Dubai

PROJECT NUMBER
269

PROJECT PHASE

DETAIL DESIGN

CONSULTANT

LOC I
لوکاب

Office M31, KIA Flagship
Building
Sheikh Zayed Rd, Al Quoz 1
P. O. Box 72928, Dubai

T +971 4 357 6573
W www.loci.ae